РОССИЙСКАЯ ФЕДЕРАЦИЯ
Общество с ограниченной ответственностью
М-Дизайн
Заказчик: ООО «ПИК-Управляющая компания»

Рабочая документация интерьеров квартир жилого дома, корпуса 2.2 с подземной автосоянкой по адресу: г. Москва, вн.тер.г. муниципальный округ Пресненский, улица Пресненский Вал, земельный участок 27/5

РАБОЧАЯ ДОКУМЕНТАЦИЯ

02/10/23-пр

Архитектурные решения интерьеров. Этаж 9/
Квартира №2.2.0910

ТИП 31

К ПРОИЗВОДСТВУ РАБОТ
25.02.2025
Главный инженер проекта
ООО ПЛАНЕТАСТРОЙ
С-77-247190
Отделкин Александр

Москва. 2024

ООО "М-Дизайн

Рабочая документация интерьеров квартир жилого дома, корпуса 2.2 с подземной автосоянкой по адресу: г. Москва, вн.тер.г. муниципальный округ Пресненский, улица Пресненский Вал, земельный участок 27/5

РАБОЧАЯ ДОКУМЕНТАЦИЯ

02/10/23-пр

Архитектурные решения интерьеров. Этаж 9/
Квартира №2.2.0910

ТИП 31

Генеральный директор: Коржавых Г. М.

ГАП Сабликов А. В.

К ПРОИЗВОДСТВУ РАБОТ
25.02.2025
Главный инженер проекта
ООО ПЛАНЕТАСТРОЙ
С-77-247190
Отделкин Александр

Москва. 2024

Состав проекта

Лист	Наименование	Раздел
1	Лист общих данных. Ведомость чертежей.	АИ
2	План монтажа перегородок	
3	План пола с указанием трасс отопления и размещением отопительных приборов	
4	План расстановки мебели и привязка инженерного оборудования	
5	Развертки стен	
6	Ведомость отделки помещений	
7	Ведомость ссылочных и прилагаемых документов	ЭОМ
8	Общие указания	
9	Однолинейная схема силового щита ЩС	
10	План розночной сети	
11	План освещения, слаботочной сети	
12	Спецификация оборудования изделий и материалов Лист 1	
13	Спецификация оборудования изделий и материалов Лист 2	
14	Общие данные Лист 1	ВК
15	Общие данные Лист 2	
16	План систем водоснабжения	
17	План систем канализации	
18	Схема системы водоснабжения	
19	Схема систем канализации	
20	Спецификация изднлий и материалов Лист 1	
21	Спецификация изднлий и материалов Лист 2	

Общие указания

1.
1.1. Разработано на основании проекта АР, рабочего проекта и технического задания от Заказчика.
1.2. За отметку 0.000 принята отметка уровня чистого пола этажа.
1.3. Стены и перегородки выполнять в соответствии с кладочными планами раздела АР.
2.
2.1. В проекте учтено расположение и количество инженерного оборудования на основании стандарта Базы Знаний ПИК.
2.2. Проектом предусмотрена уточняющая привязка/перенос следующего инженерного оборудования:
-- Радиаторов отопления;
-- Домофона.
2.3 Привязка и количество прочего инженерного оборудования учтены без изменений.
2.4 Дополнительно проектом предусмотрены открытая разводка труб ХГВС к сантехническому оборудованию и кабелей к светильникам, скрытая разводка к розеткам и выключателям.
3
2.1. Проектом предусмотрены черновая отделка пола, стен, потолка.
2.2. В полах помещений санузлов предусмотрено устройство гидроизоляции.
4.
4.1. Условные обозначения указаны на листах основного комплекта рабочих чертежей.
4.2. Все размеры даны в миллиметрах.
4.3. Размеры отмеченные (*) даны ориентировочно и могут быть откорректированы по месту.

К ПРОИЗВОДСТВУ РАБОТ
25.02.2025
Главный инженер проекта
ООО ПЛАНЕТАСТРОЙ
С-77-247190
Отделкин Александр

Согласовано

Взам. инв №

Подп и дата

Инв. № подл

					2024	Заказчик: ООО «ПИК-УК»
						Рабочая документация интерьеров квартир жилого дома, корпуса 2.2 с подземной автосоянкой по адресу: г. Москва, вн.тер.г. муниципальный округ Пресненский, улица Пресненский Вал, земельный участок 27/5
Изм.	Кол. уч.	Лист	№ док.	Подпись	Дата	
Архитектор		СабликовА. В.				Архитектурные решения интерьеров. Этаж 9/ Квартира №2.2.0910
						Лист общих данных. Ведомость чертежей.


Стадия	Лист	Листов
Р	1	

М-Дизайн

Копировал

Формат

План монтажа перегородок

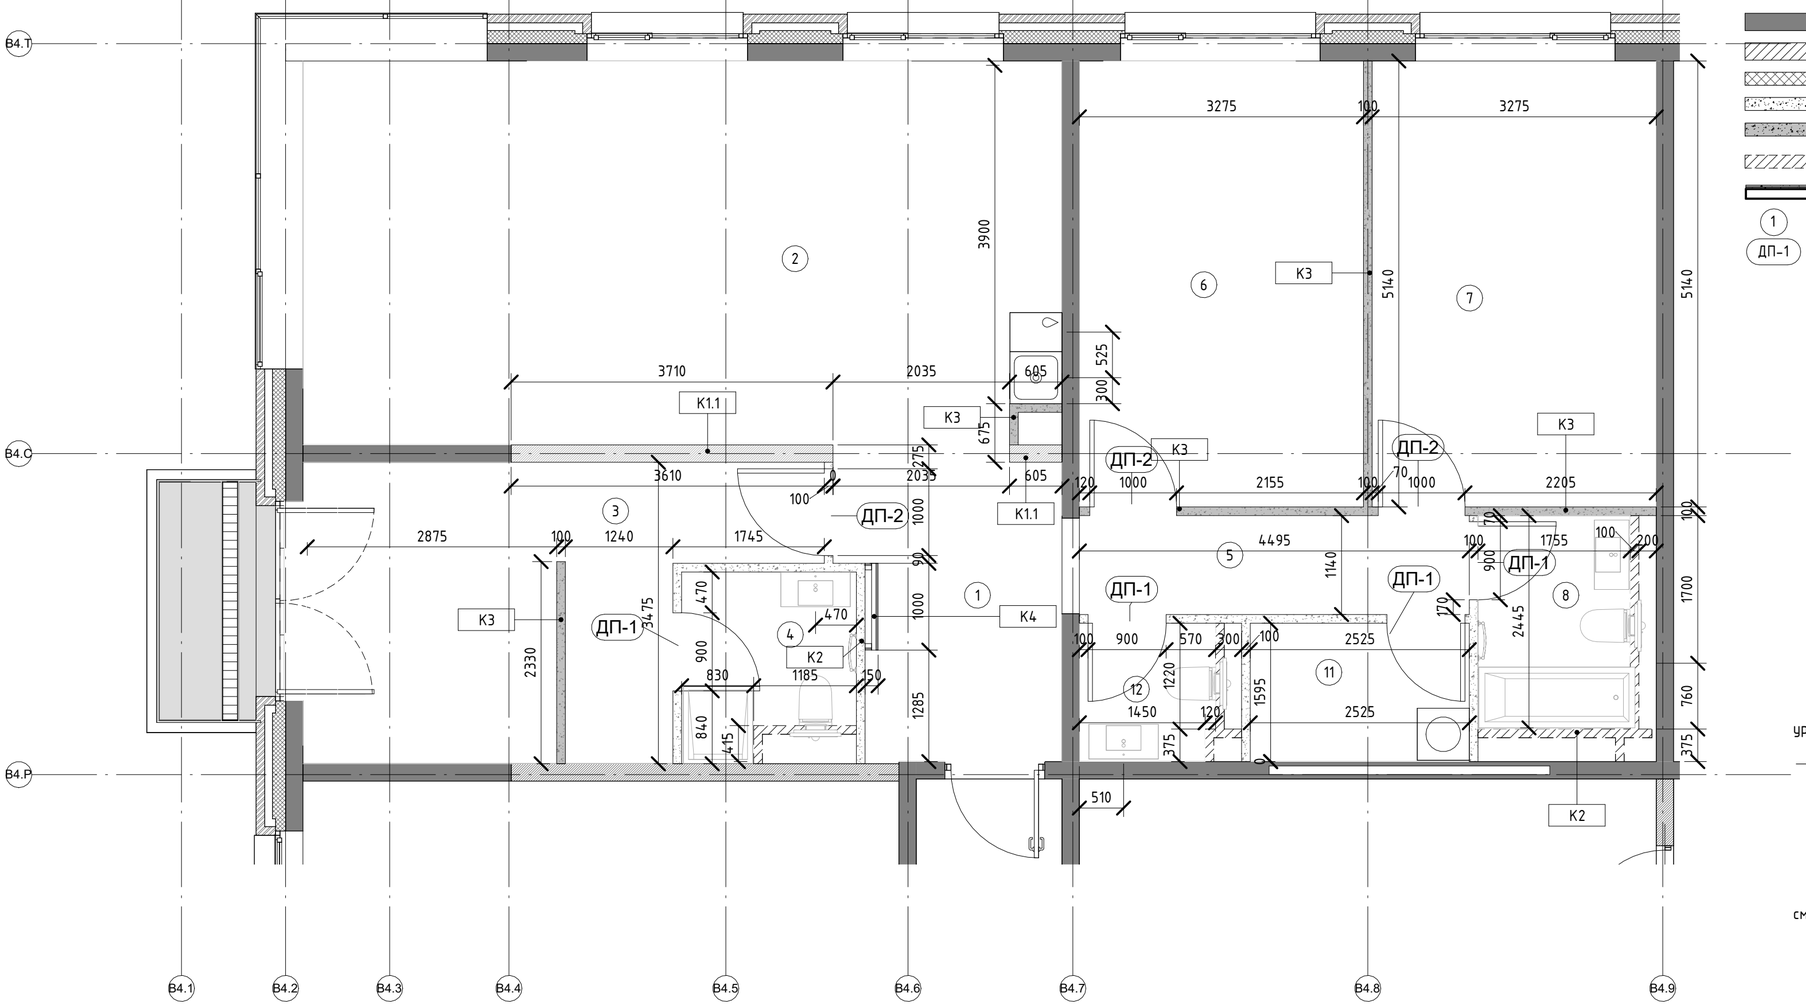


Условные обозначения


- Стены из монолитного железобетона
- Стены из газобетонного блока
- Утеплитель
- Пазогребневый блок влагостойкий
- Пазогребневый блок
- Пазогребневый блок влагостойкий h-500мм (в один блок)
- ГКЛ перегородка
- (1) Маркировка помещения
- ДП-1 Маркировка дверного проема

Экспликация помещений


№	Наименование	Площадь м2
1	Холл	8.28
2	<варианты>	38.63
3	Жилая комната	16.55
4	Жилая комната	3.93
5	<варианты>	5.12
6	<варианты>	16.83
7	Жилая комната	16.83
8	С/У	4.31
9	Гардероб	0.00
11	Постирочная	4.14
12	С/У	2.47
	ИТОГО:	117.11

Схемы подвода ХГВС к сантех. оборудованию

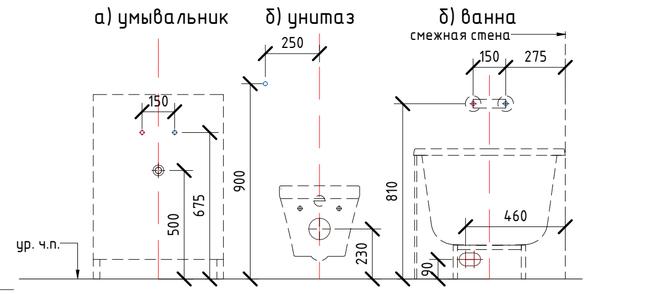

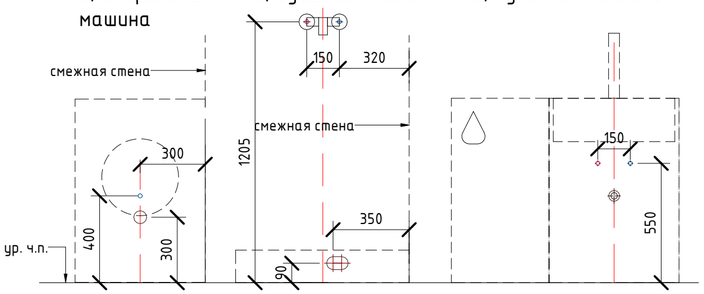

Отделка откосов окон ГСП-Н2 в 1-н слой, с выравниванием

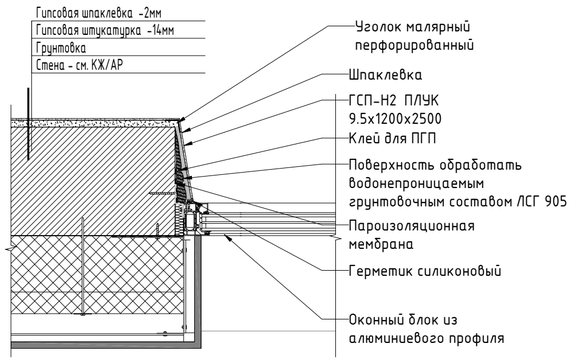

Ведомость проемов и отверстий

Обозначение	Размеры (ШхВ)	отметка ур.ч.п.	Кол-во	Примечание
ДП-1	900х2500	0.100	4	
ДП-2	1000х2500	0.100	3	

Ведомость межкомнатных перегородок

Марка по АР	Описание по АР	Объем м3	Примечание
К1.1	Газобетонный блок	2.69 м³	
К2	Пазогребневые плиты влагостойкие 667х500х100 мм, полнотелые, тип прочности А, плотности D (Волма или аналог)	4.48 м³	
К3	Пазогребневые плиты 667х500х100 мм, полнотелые, тип прочности А, плотности D (Волма или аналог)	4.21 м³	
К4	ГКЛ перегородка (2 слоя ГКЛ)	0.23 м³	

Примечания

1. Стены и межкомнатные перегородки выполнить по проекту АР.
2. За относительную отметку 0,000 принять отметку чистого пола этажа.
3. Чертеж содержит уточняющие данные габаритов и привязку проемов и отверстий.
4. Размеры отмеченные звездочкой (*) требуют уточнения по месту.

К ПРОИЗВОДСТВУ РАБОТ
25.02.2025
Главный инженер проекта
Отделкин Александр

					2024
Изм.	Кол. уч.	Лист	№ док.	Подпись	Дата
Архитектор		СабликовА. В.			

Заказчик: ООО «ПИК-УК»

Рабочая документация интерьеров квартир жилого дома, корпуса 2.2 с подземной автосоянкой по адресу: г. Москва, вн.тер.г. муниципальный округ Пресненский, улица Пресненский Вал, земельный участок 27/5

Архитектурные решения интерьеров. Этаж 9/ Квартира №2.2.0910

Стадия	Лист	Листов
Р	2	

План монтажа перегородок

М-Дизайн

Согласовано

Взам. инв №


Подп. и дата

Инв. № подл

Копировал

Формат

План пола с указанием трасс отопления и размещением отопительных приборов.

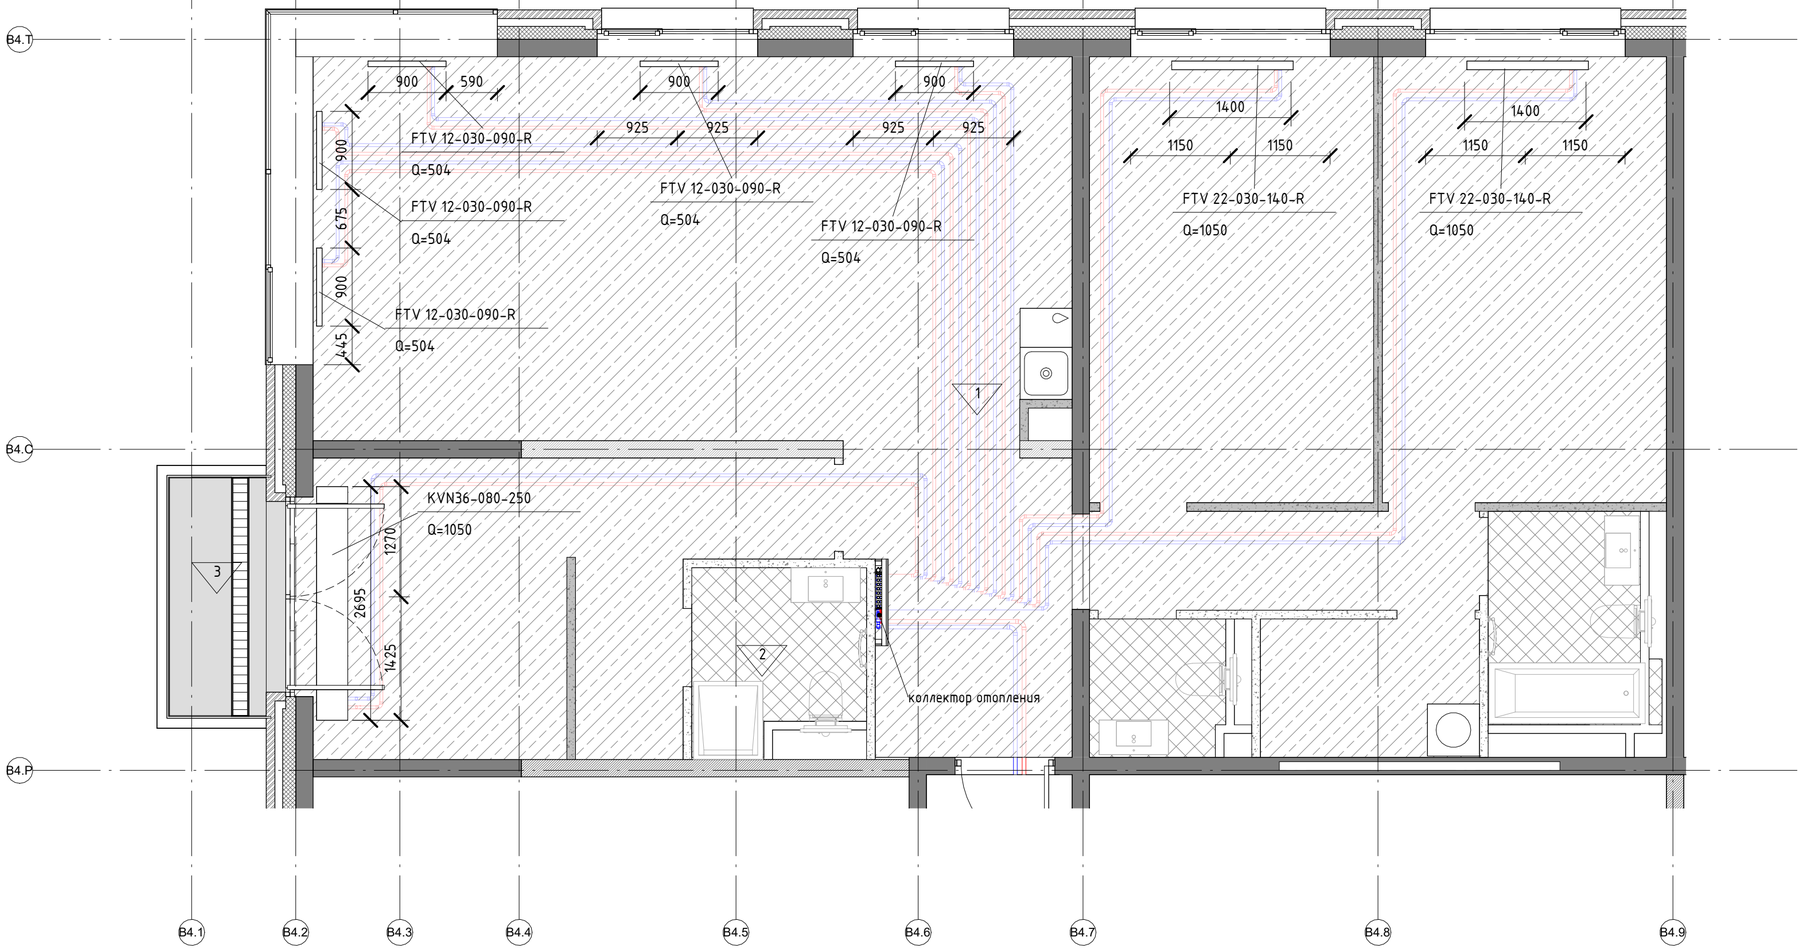

Экспликация помещений		
№	Наименование	Площадь м2
1	Холл	8.28
2	<варианты>	38.63
3	Жилая комната	16.55
4	Жилая комната	3.93
5	<варианты>	5.12
6	<варианты>	16.83
7	Жилая комната	16.83
8	С/У	4.31
9	Гардероб	0.00
11	Постирочная	4.14
12	С/У	2.47
	ИТОГО:	117.11

Условные обозначения:

1 – Маркировка помещения

1 – Тип пола (по АИ)

– Тип 1
Шумоизоляция 20мм, стяжка 60мм

– Тип 2
Полимерная гидроизоляция с заводом на стены 200мм, стяжка 58мм

– Отопление. подача

– Отопление. обратка

KVN36-080-225 Q=950
конвектор впольный
ширина
глубина
длина
мощность

FTV 12-030-110-R Q=650
радиатор настенный
ширина
высота
длина
мощность

Примечания:

1. За относительную отметку 0,000 принять отметку чистого пола этажа.
2. Толщину отделочного слоя принять 20 мм.
3. Общий пирог пола с отделкой для жилых комнат и коридоров принять 110 мм, для санузлов – 80 мм.
4. Финишная отделка выполняется собственником.
5. В санузлах выполнить полимерную гидроизоляцию с заводом на стены 200мм.
6. Ведомость материалов – смотреть лист 8.
7. Устройство уклона на террасах и лоджиях принять согласно разделу АР.

К ПРОИЗВОДСТВУ РАБОТ
25.10.2024
Главный инженер проекта
ООО ПЛАНЕТАСТРОЙ
С-77-247190
Отделкин Александр

					2024	Заказчик: ООО «ПИК-УК»	
						Рабочая документация интерьеров квартир жилого дома, корпуса 2.2 с подземной автосоянкой по адресу: г. Москва, вн.тер.г. муниципальный округ Пресненский, улица Пресненский Вал, земельный участок 27/5	
Изм.	Кол. уч.	Лист	№ док.	Подпись	Дата		
Архитектор		СабликовА. В.				Архитектурные решения интерьеров. Этаж 9/ Квартира №2.2.0910	Стадия: Р; Лист: 3; Листов:
						План пола с указанием трасс отопления и размещением отопительных приборов.	М-Дизайн

Согласовано

Взам. инв №

Подп. и дата

Инв. № подл

Копировал


Формат

План расстановки мебели и оборудования



Экспликация помещений		
№	Наименование	Площадь м2
1	Холл	8.28
2	<варианты>	38.63
3	Жилая комната	16.55
4	Жилая комната	3.93
5	<варианты>	5.12
6	<варианты>	16.83
7	Жилая комната	16.83
8	С/У	4.31
9	Гардероб	0.00
11	Постирочная	4.14
12	С/У	2.47
	ИТОГО:	117.11

Схемы подключения ХГВС к сантех оборудованию

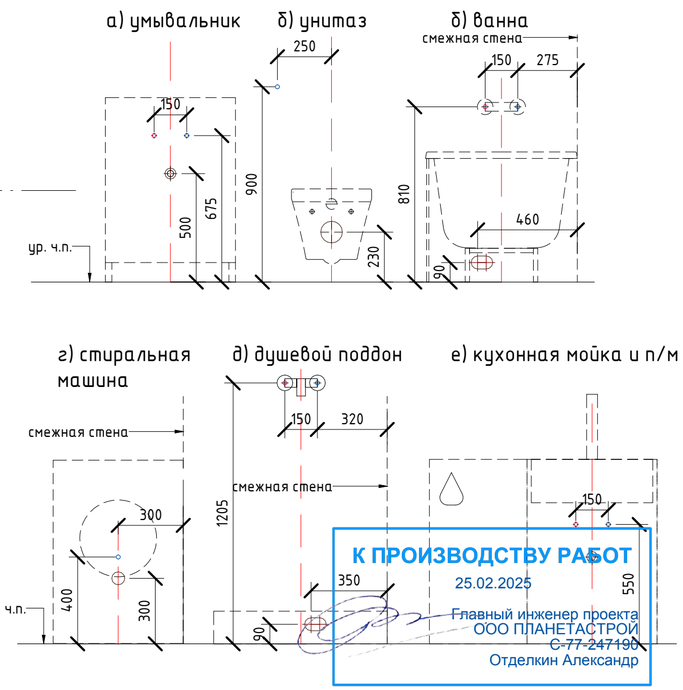

К ПРОИЗВОДСТВУ РАБОТ
25.02.2025
Главный инженер проекта
ООО ПЛАНЕТАСТРОЙ
С-77-247190
Отделкин Александр

Согласовано

Взам. инв №

Подп. и дата

Инв. № подл

Изм.	Кол. уч.	Лист	№ док.	Подпись	Дата
					2024

Заказчик: ООО «ПИК-УК»


Рабочая документация интерьеров квартир жилого дома, корпуса 2.2 с подземной автосоянкой по адресу: г. Москва, вн.тер.г. муниципальный округ Пресненский, улица Пресненский Вал, земельный участок 27/5

Архитектор	СабликовА. В.	Архитектурные решения интерьеров. Этаж 9/ Квартира №2.2.0910	Стадия: Р; Лист: 4; Листов:
		План расстановки мебели и оборудования	М-Дизайн


Копировал

Формат


1-1

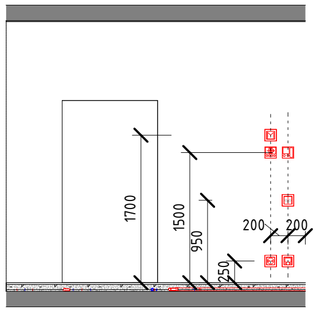


1-2

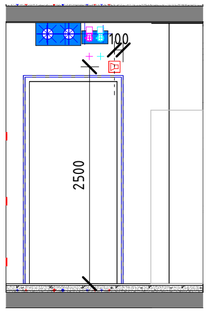


1-3

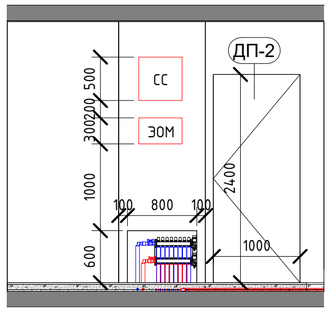


2-1

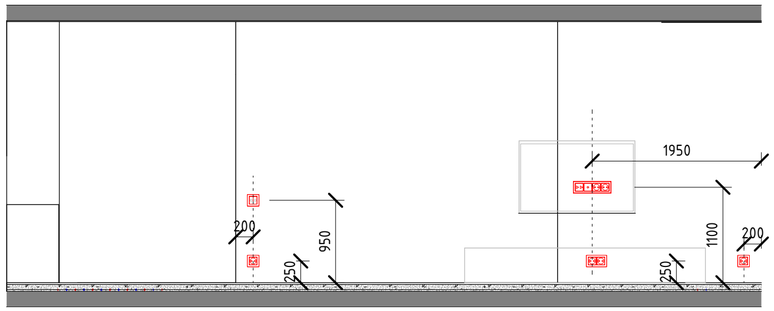


2-2

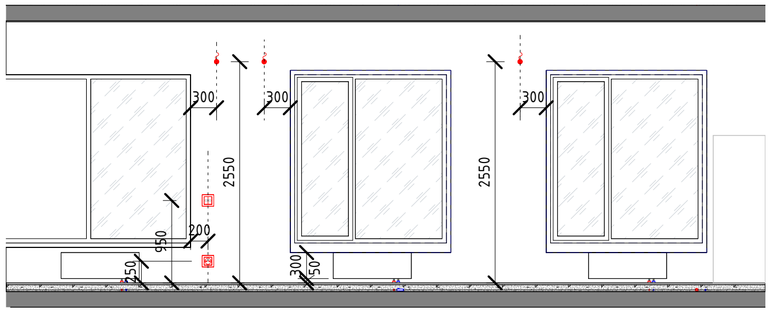


2-3

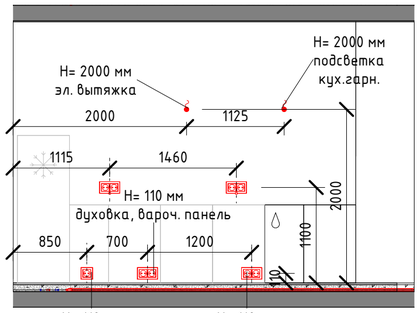


3-1

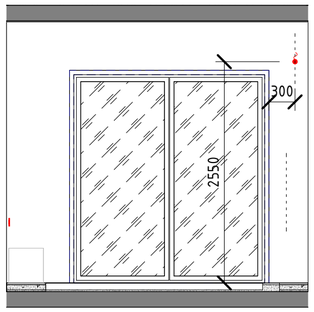


3-2

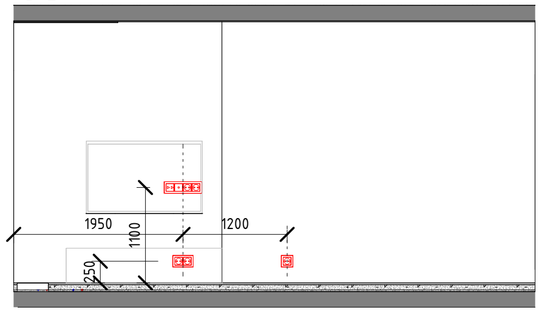


3-3

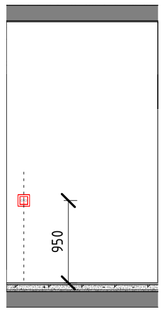


3-4

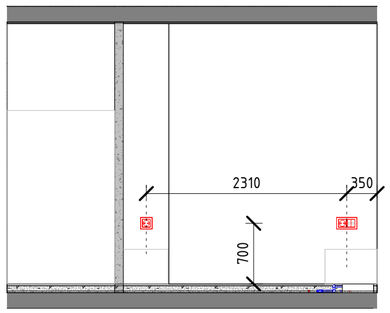


3-5

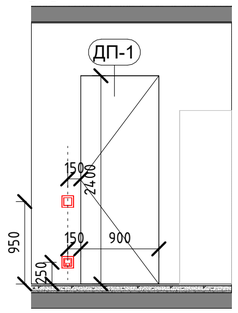


5-1

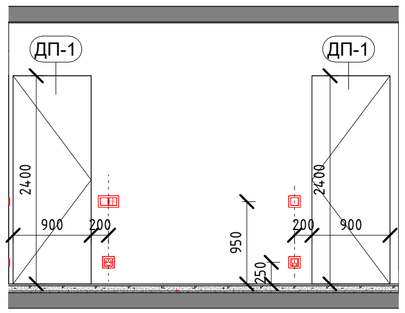


6-1

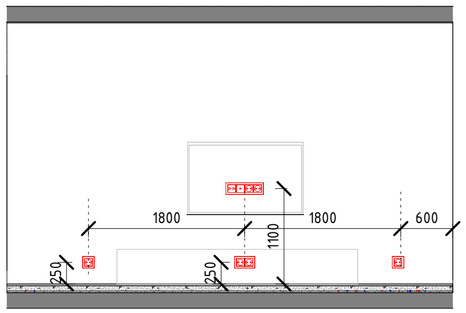


6-2

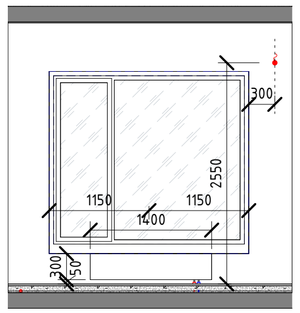


6-3

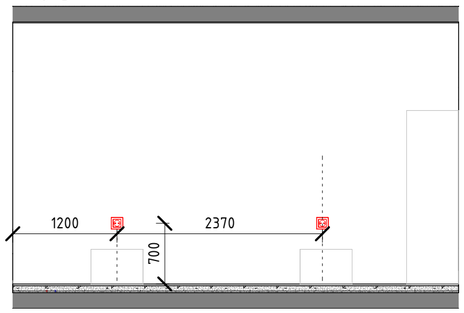


6-4

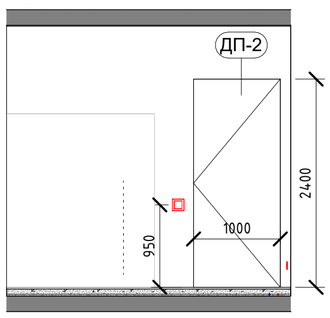


7-1

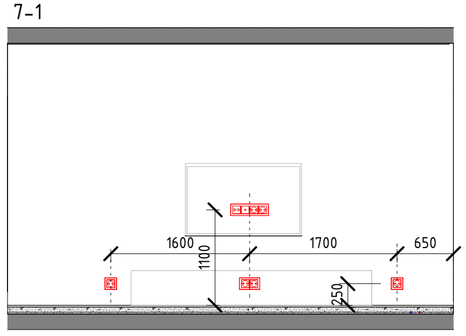


7-2

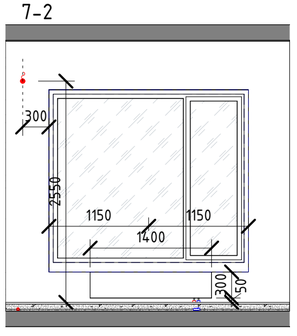

7-3

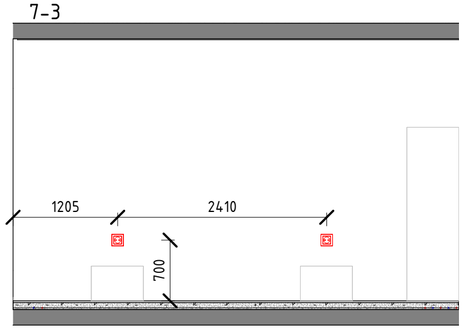

7-4

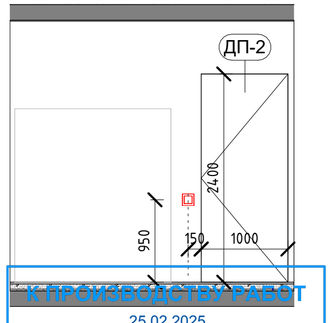

Условные обозначения:

- Розетка силовая 220V (+0.250 от ур. ч.п. Изм. см. чертеж)
- Фальш-розетка + кабель-канал (40x25)
- Розетка RJ45 x2 (h см. чертеж)
- Розетка TV
- Расцепитель на группы вентиляции и кондиционирования
- Термостат для теплого пола
- Домофон
- Выключатель одноклавишный
- Выключатель двухклавишный
- Звонок
- Эл. вывод

Примечание:

1. Чертеж смотреть совместно с Планом электрических и слаботочных сетей, лист 05.
2. Все отметки до центра рамки розеток и включателей даны от уровня чистого пола.
3. Все розетки устанавливаются на высоте 250 мм от у.ч.п., кроме специально отмеченных.
4. Блоки розеток установить горизонтально, изменения см. чертеж.
5. Оконечное оборудование не устанавливается, монтируются только подрозетники.
8. Штроба в стенах заделывается штукатуркой.
7. Предусмотреть закладные элементы в стенах для установки розеток и выключателей.
8. Электрические выводы необходимо защитить специальным клеммником.
9. Электрические силовые выводы, расположенные в заводской коробке, закрыть крышкой распаячной
10. Подрозетники увеличенной глубины в местах установки выключателей для коммутации линий освещения без применения распаячных коробок за потолком.
11. Встроенный слаботочный щит для размещения ONT. В щитке предусмотреть патч панель и силовую розетку 220В. Кабельная разводка UTP cat.5e с установкой подрозетников в местах размещения TV и рабочих столов.
12. Разводка слаботочных сетей (IP-TV, интернет, домофон (разводка до квартиры, оставляем провод в подрозетнике))

К ПРОИЗВОДСТВУ РАБОТ
25.02.2025
Главный инженер проекта
ООО ПЛАНЕТАСТРОЙ
С-77-247190
Отделкин Александр

Изм.	Кол. уч.	Лист	№ док.	Подпись	Дата
					2024
Архитектор		СабликовА. В.			

Заказчик: ООО «ПИК-УК»

Рабочая документация интерьеров квартир жилого дома, корпуса 2.2 с подземной автосоянкой по адресу: г. Москва, вн.тер.г. муниципальный округ Пресненский, улица Пресненский Вал, земельный участок 27/5

Архитектурные решения интерьеров. Этаж 9/ Квартира №2.2.0910

Стадия	Лист	Листов
Р	5	

Развертки стен

М-Дизайн

Согласовано

Взам. инв №





Подп. и дата

Инв. № подл




Копировал

Формат

Спецификация отделки стен

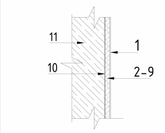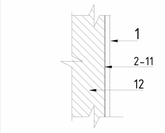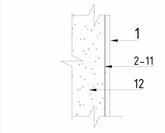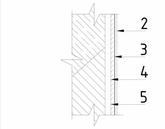Назначение	Схема конструкции	Данные элементов отделки	Площадь, м2	Номер помещения	Примечание
Квартира (холл, жилые комнаты, кухня)		1. Финишная отделка (выполняется собственником) 2. Грунтовка (ГС7) 3. Финишная шпатлевка (качество поверхности К4) – до 1мм 4. Грунтовка 5. Стеклохолст с использованием специального клея 6. Грунтовка 7. Гипсовая шпатлевка в 2 слоя (качество поверхности К3) – до 3мм 8. Грунтовка 9. Штукатурка улучшенная гипсовая по маякам – до 20мм 10. Грунтовка (ГС4)/бетонконтакт 11. Основание – Монолитный железобетон	112.45	1, 2, 3, 5, 6, 7	
Квартира (холл, жилые комнаты, кухня)		1. Финишная отделка (выполняется собственником) 2. Грунтовка (ГС7) 3. Финишная шпатлевка (качество поверхности К4) – до 1мм 4. Грунтовка 5. Стеклохолст с использованием специального клея 6. Грунтовка 7. Гипсовая шпатлевка в 2 слоя (качество поверхности К3) – до 3мм 8. Грунтовка 9. Штукатурка улучшенная гипсовая по маякам в 2 слоя по сетке – до 30мм 10. Грунтовка (ГС2) 11. Грунтовка глубокого проникновения (ГС1) 12. Основание – Газобетонные блоки	32.47	1, 2, 3	
Квартира (холл, жилые комнаты, кухня)		1. Финишная отделка (выполняется собственником) 2. Грунтовка (ГС7) 3. Финишная шпатлевка (качество поверхности К4) – до 1мм 4. Грунтовка 5. Стеклохолст с использованием специального клея 6. Грунтовка 7. Гипсовая шпатлевка в 2 слоя (качество поверхности К3) – до 3мм 8. Грунтовка 9. Штукатурка улученная гипс. по маякам по сетке – до 10мм 10. Грунтовка (ГС2) 11. Грунтовка глубокого проникновения (ГС1) 12. Основание – ПГП.	125.12	<варианты>	
Квартира (оконные откосы)		1. Финишная отделка (выполняется собственником) 2. Грунтовка (ГС7) 3. Гипсовая шпаклевка в 2 слоя (качество поверхности К4) – до 2мм 4. Грунтовка глубокого проникновения 5. Основание – ГСП-Н2 9.5 мм	15.08	2, 3, 6, 7	

Спецификация отделки полов

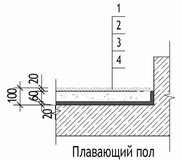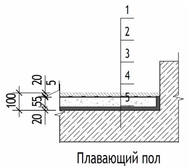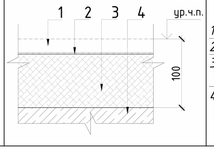Назначение	Тип пола	Схема конструкции	Состав пола	Площадь, м2	Номер помещения	Примечание
Квартира (холл, жилые комнаты, кухня)	1	 Плавающий пол	1. Финишная отделка (выполняется собственником) – 20мм 2. Стяжка из ц/п раствора М150 (армированная фиброволокном) –60мм 3. Шумоизолирующая мембрана Шумостоп (или аналог) – 20мм 4. Монолитная ж.б. плита – см. раздел КЖ	107.19	1, 2, 3, 5, 6, 7, 9, 11	Финишная отделка не выполняется
Квартира (санузлы)	2	 Плавающий пол	1. Финишная отделка (выполняется собственником) – 20мм 2. Гидроизоляция цементная Ceresit 65 (или аналог) завести на стены на 300мм – 5мм 3. Стяжка из ц/п раствора М150 (армированная фиброволокном) –55мм 4. Шумоизоляционная мембрана Шумостоп (или аналог) – 20мм 5. Монолитная ж.б. плита – см. раздел КЖ	10.88	4, 8, 12	Финишная отделка не выполняется
балкон	3		1. Финишная отделка (выполняется собственником) – 20мм 2. Гидроизоляция обмазочная битумная Гост 30693-2009 – 2 мм 3. Стяжка из ц/п раствора М150 по уклону, армированная сеткой 4Bpi с ячейкой 100х100 мм – 78 мм – 2мм 4. Ж/б плита перекрытия	3.07		Финишная отделка не выполняется. Уклон – см альбом АР

Спецификация отделки потолков

Назначение	Тип потолка	Состав отделки	Площадь, м2	Номер помещения	Примечание
Квартира (холл, жилые комнаты, кухня, санузлы)	пт.1	1. Финишная отделка (выполняется собственником) 2. Грунтовка глубокого проникновения 3. Зачистка	117.14	1, 2, 3, 4, 5, 6, 7, 8, 9, 11, 12	

К ПРОИЗВОДСТВУ РАБОТ
25.02.2025
Главный инженер проекта
ООО ПЛАНЕТАСТРОЙ
С-77-247190
Отделкин Александр

Примечания:

1. Все черновые материалы, указанные в проекте, могут быть заменены на аналогичные при сохранении основных свойств и характеристик.
2. При проведении малярных работ дополнительно могут применяться малярная сетка, малярные уголки, малярные ограничители и другие материалы, необходимые и достаточные для обеспечения высококачественной отделки и ровных углов.
3. Технология отделочных работ может быть изменена по согласованию с заказчиком.
4. Указано проектное количество материала, без учета расходного запаса и количество слоев покрытия.
5. Отделка сан. узлов выполняетс собственником

					2024
Изм.	Кол. уч.	Лист	№ док.	Подпись	Дата

Заказчик: ООО «ПИК-УК»

Рабочая документация интерьеров квартир жилого дома, корпуса 2.2 с подземной автосоянкой по адресу: г. Москва, вн.тер.г. муниципальный округ Пресненский, улица Пресненский Вал, земельный участок 27/5

Архитектор	СабликовА. В.	Архитектурные решения интерьеров. Этаж 9/ Квартира №2.2.0910	Стадия: Р; Лист: 6; Листов:
		Ведомость отделки помещений	М-Дизайн

Согласовано

Взам. инв №

Подп. и дата

Инв № подл

Копировал

Формат

ВЕДОМОСТЬ ССЫЛОЧНЫХ И ПРИЛАГАЕМЫХ ДОКУМЕНТОВ

Обозначение	Наименование	Примечание
ГОСТ Р 21.101-2020	Основные требования к проектной и рабочей документации	
ГОСТ 21.110-2013	Правила выполнения спецификации оборудования, изделий и материалов	
ГОСТ 2.702-2011	Правила выполнения электрических схем	
ГОСТ 21.501-2018	Правила выполнения архитектурно-строительных рабочих чертежей	
ГОСТ 21.210-2014	Изображения условные графические электрооборудования и проводок на планах	
ГОСТ 31565-2012	Кабельные изделия. Требования пожарной безопасности	
ГОСТ 30331.1-2013	Электроустановки низковольтные	
ПУЭ 7 издание	Правила устройства электроустановок	
СП-31-110-2003	Проектирование и монтаж электроустановок жилых и общественных зданий	
СП 76.13330.2016	Электротехнические устройства	
ПОСТАНОВЛЕНИЕ от 23 июля 2001 года N 80	О принятии строительных норм и правил Российской Федерации "Безопасность труда в строительстве. Часть 1. Общие требования"	
ФЗ от 22.07.2008 №123-ФЗ	Технический регламент о требованиях пожарной безопасности.	
	Прилагаемые документы	
02/10/23-ЭОМ.С	Спецификация оборудования, изделий и материалов	на 2 листах

К ПРОИЗВОДСТВУ РАБОТ
25.02.2025
Главный инженер проекта
ООО ПЛАНЕТАСТРОЙ
С-77-247190
Отделкин Александр

В настоящей рабочей документации все технические решения по сооружениям, конструкциям, оборудованию и технологической части приняты и разработаны в полном соответствии с действующими на дату выпуска проекта нормами и правилами, включая правила пожаро- и взрывобезопасности.

При соблюдении правил технической эксплуатации, а так же требований техники безопасности, пожаро- и взрывобезопасности эксплуатации сооружений по данному проекту безопасна.

Главный инженер проекта /

Взам. инв.N | Подпись и дата | Инв.N подл.

Изм.	Кол.	Лист	№ док.	Подпись	Дата	02/10/23-ЭОМ	Лист 7

Формат А4

Общие указания

1. Введение.

В настоящей рабочей документации предусмотрен монтаж розеточной сети и освещения квартиры повышенной комфортности.

2. Источники электроснабжения. Напряжения.

Границей проектирования являются клеммы вводного автоматического выключателя силового щита ЩС.

Напряжения:

380/220 В – напряжение сети низкого напряжения силовых потребителей и электроосвещения.

3. Объем реконструкционных работ.

В объем проектирования входит:

– силовой щит квартиры;

– кабельные линии силовой и слаботочной части.

Кабельная продукция

Марка кабельной продукции выбрана согласно ГОСТ 31565-2012 (индекс -LS для жилых зданий), сечения кабелей выбраны согласно ГОСТ 31996-2012.

4. Обозначения:

Шины должны быть обозначены:

При переменном трехфазном токе: шины фазы А – желтым, фазы В – зеленым, фазы С – красным цветами.

Нулевые рабочие (нейтральные) проводники обозначаются буквой N и голубым цветом. Проводники защитного заземления должны иметь буквенное обозначение PE и цветовое обозначение чередующимися продольными или поперечными полосами одинаковой ширины желтого и зеленого цветов. Допускается выполнять цветовое обозначение не по всей длине шин, только цветовое или только буквенно-цифровое обозначение либо цветовое в сочетании с буквенно-цифровым в местах присоединения шин.

5. Освещение

Проектом предусматривается рабочее освещение. Расключение кабелей выполнить в подрозетниках с увеличенной глубиной монтажа. Прокладка кабеля осуществляется в гофротрубе открыто по перекрытию и скрыто в стенах в штробе. Светильники устанавливаются Заказчиком и в данном проекте не предусматриваются.

6. Розеточные сети

Расключение кабелей выполнить в подрозетниках с увеличенной глубиной монтажа. К щиту ЩС каждая отходящая линия выполняется одним кабелем, подключение нескольких электроприемников одной группы выполняется через подрозетники шлейфом. Прокладка кабеля осуществляется в гофротрубе открыто по перекрытию и скрыто в стенах в штробе. Электроприемники устанавливаются Заказчиком и данным проектом не предусматриваются.

7. Техника безопасности и охрана труда

Проектом указывается на необходимость строго соблюдать нормы и правила по технике безопасности и охране труда в процессе выполнения строительно-монтажных работ, последующей эксплуатации и технического обслуживания электроустановок. При этом обращается особое внимание на необходимость руководствоваться следующими документами:

– правила устройства электроустановок (ПУЭ-7 издание);

– правила по охране труда при эксплуатации электроустановок (ПОТЭУ);

– правила эксплуатации электроустановок (ПТЭЭП от 12 августа 2022 г. № 811).

Монтажные работы проводить в соответствии с ПУЭ, и соблюдением норм СП 76.13330.2016, с заводскими инструкциями по монтажу и эксплуатации оборудования.

К ПРОИЗВОДСТВУ РАБОТ
25.02.2025
Главный инженер проекта
ООО ПЛАНЕТАСТРОЙ
С-77-247190
Отделкин Александр

Взам. инв.N

Подпись и дата

Инв.N подл.

Изм.	Кол.	Лист	№ док.	Подпись	Дата	02/10/23- ЭОМ	Лист 8

Формат А4


U = ~380/220В
Руст.=26,7кВт
Кс=0,6
Рр =16,1кВт
Iр = 25,8 А
cosф=0,95

Вводный аппарат

Шинопровод

Авт. выключатель

Отх. линия (кабельная)

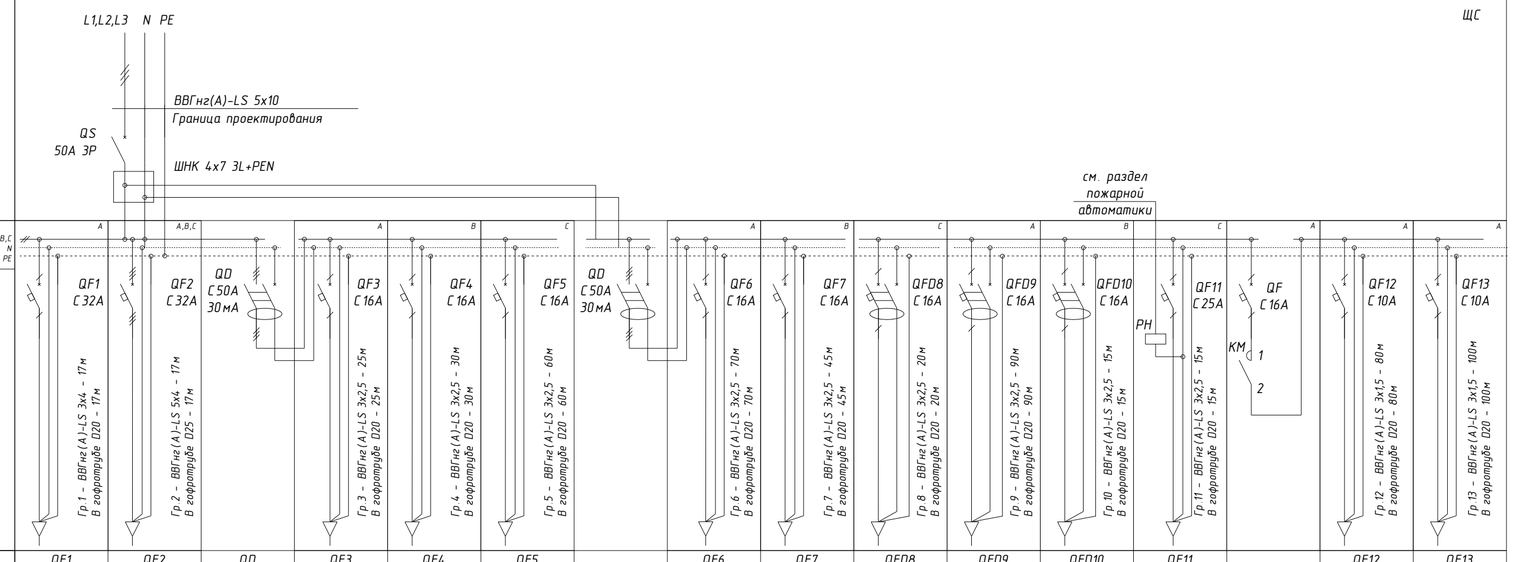


Наименование авт. выкл.	QF1	QF2	QD	QF3	QF4	QF5		QF6	QF7	QFD8	QFD9	QFD10	QF11		QF12	QF13
Номинальный ток, А	32	32	50	16	16	16		16	16	16	16	16	25		10	10
Ток утечки			30					30	30	30	30	30	–			
Рн, кВт	4	8,5		2	1	1		1	1	2,5	0,5	2	3		0,1	0,1
Iном, А	19,2	13,6		9,6	5,4	5,4		4,8	4,8	13,4	2,4	9,6	16,1		0,5	0,5
Наименование электромеханизма по плану	Духовка электрическая	Плита электрическая		Розетки кухня, электроштора	Розетки кухня	Розетки кухня (зона отдыха)		Розетки коридор, звонок, ЩСС, спальня 1	Розетки спальня 2,3	Стиральная машина + сушилка	Санузлы + теплый пол	Бойлер	Приточно-вытяжная вентиляция, вытяжка	Освещение квартиры	Освещение пом.1-4	Освещение пом.5,6

Потребность кабелей

Марка, число и сечение жил	Длина
ВВГнг(А)-LS 5х4	17
ВВГнг(А)-LS 3х4	17
ВВГнг(А)-LS 3х2,5	370
ВВГнг(А)-LS 3х1,5	180

Потребность труб

Наименование	Кол-во, м
Гофротруба ПВХ D20	567
Гофротруба ПВХ D25	17

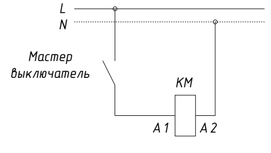


К ПРОИЗВОДСТВУ РАБОТ
25.02.2025
Главный инженер проекта
ООО ПЛАНЕТАСТРОЙ
С-77-247190
Отделкин Александр

Изм.	Кол.уч.	Лист	№ док.	Подп.	Дата	02/10/23-ЭОМ			
						Рабочая документация интерьеров квартир жилого дома, корпуса 2.2 с подземной автостоянкой по адресу: г. Москва, вн. тер. г. муниципальный округ Пресненский, ул. Пресненский Вал, земельный участок 27/5			
Разработал						Система электроснабжения. Освещение	Стадия	Лист	Листов
							Р	9	
Н. Контр.						Однолинейная схема силового щита ЩС	М-Дизайн		


Взам. инв.N | Подпись и дата | Инв.N подл.

Формат А4х3

План расстановки розеточной сети

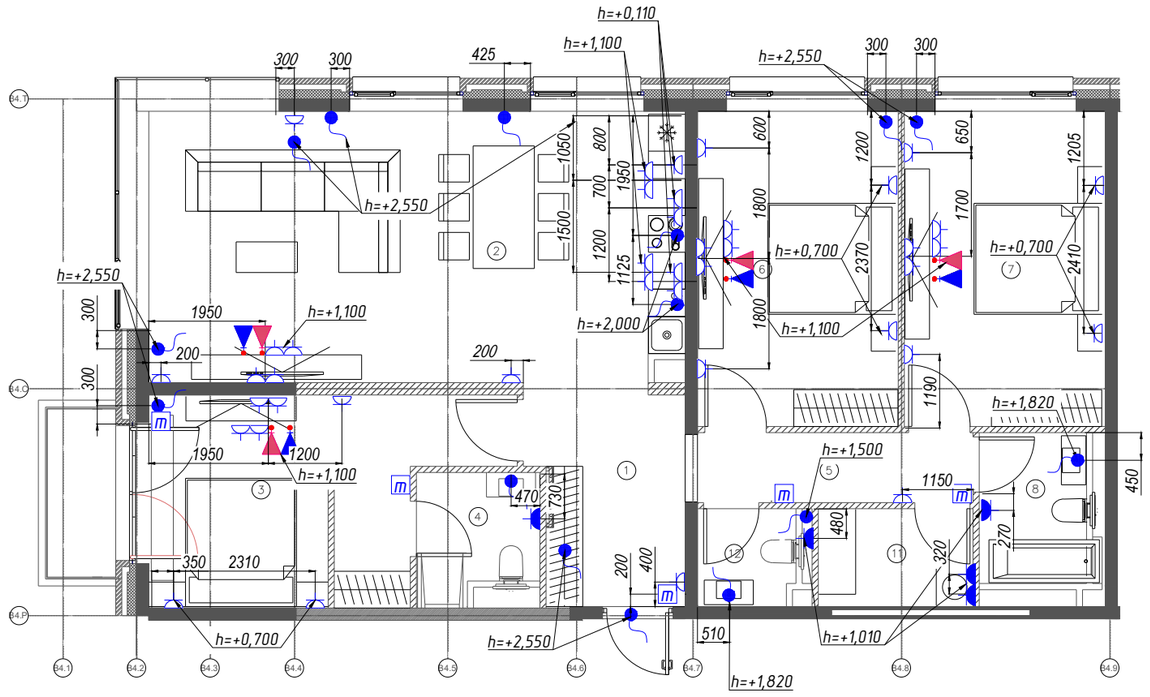


План прокладки кабельных трасс розеточной сети

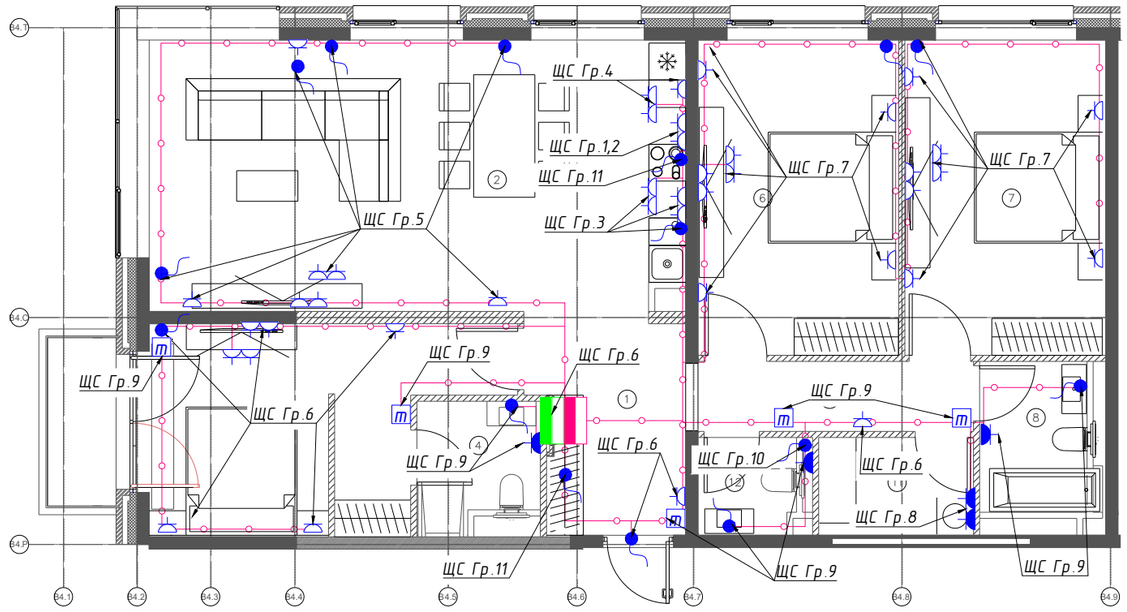

ЭТАЖ 9

ТИП 31

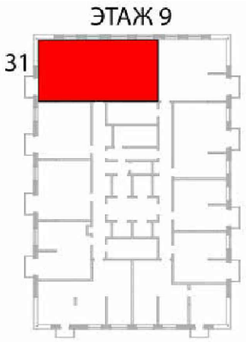


Условные обозначения

- Щит силовой ЩС
- Кабельный вывод
- Фальшрозетка (см. раздел АР)
- Розетка 220В 16А скрытой установки
- Розетка 220В 16А влагостойкая скрытой установки
- Информационная розетка RJ45 cat.5e
- ТВ розетка
- Кабель силовой в гофротрубе D20 по перекрытию

Примечание:

1. Высота до центра розетки 250мм от УЧП, если не указано иное.
2. Опуски кабеля к розеткам и кабельным выводам выполнить вертикально по стенам скрыто в штробе.
3. Запас кабеля в подрозетниках не менее 100мм
4. Розетки, подключенные к одной группе проложить шлейфом без распределительных коробок.
5. Для подключения электроплиты и духового шкафа (ЩС Гр.1, 2) оставить запас кабеля по 2 метра
6. Для подключения вытяжки оставить запас кабеля 1 метр.

Система уравнивания потенциалов в санузлах

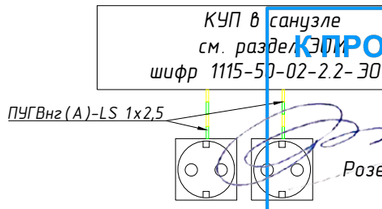


К ПРОИЗВОДСТВУ РАБОТ
25.02.2025
Главный инженер проекта
ООО ПЛАНЕТАСТРОЙ
С-77-247190
Отделкин Александр

						02/10/23-ЭОМ		
						Рабочая документация интерьеров квартир жилого дома, корпуса 2.2 с подземной автостоянкой по адресу: г. Москва, вн. тер. г. муниципальный округ Пресненский, ул. Пресненский Вал, земельный участок 27/5		
Изм.	Кол.уч.	Лист	№ док.	Подп.	Дата			
Разработал						Система электроснабжения. Освещение	Стадия: Р	Лист: 10 / Листов:
Н. Контр.						План розеточной сети	М-Дизайн	


Взам. инв.N | Подпись и дата | Инв.N подл.

Формат А3

План освещения

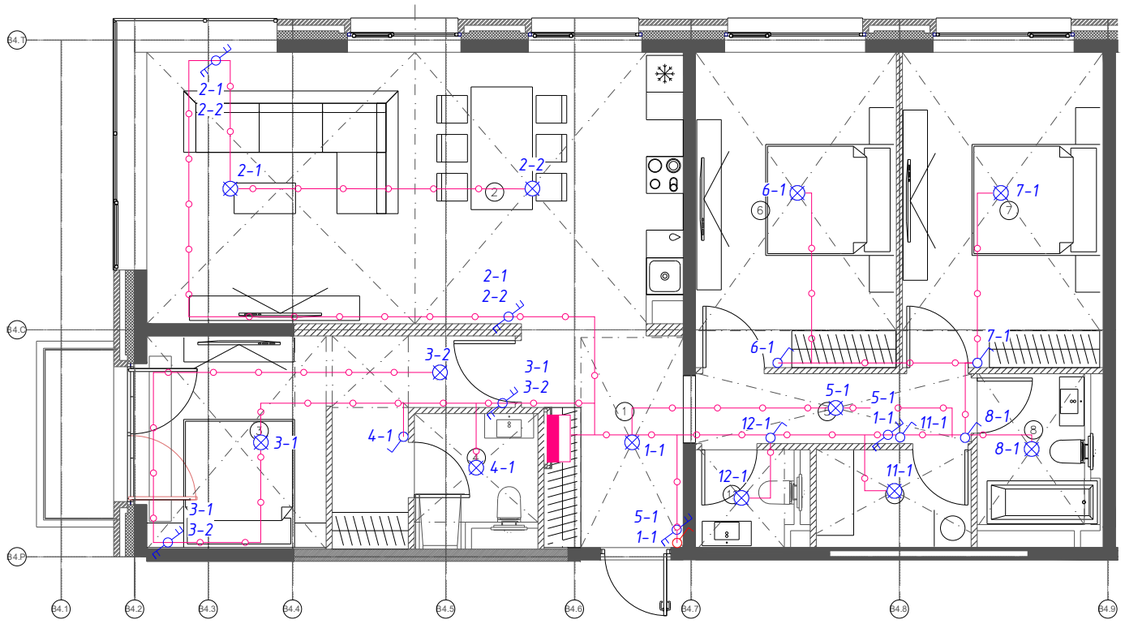


План прокладки кабельных трасс слаботочной сети

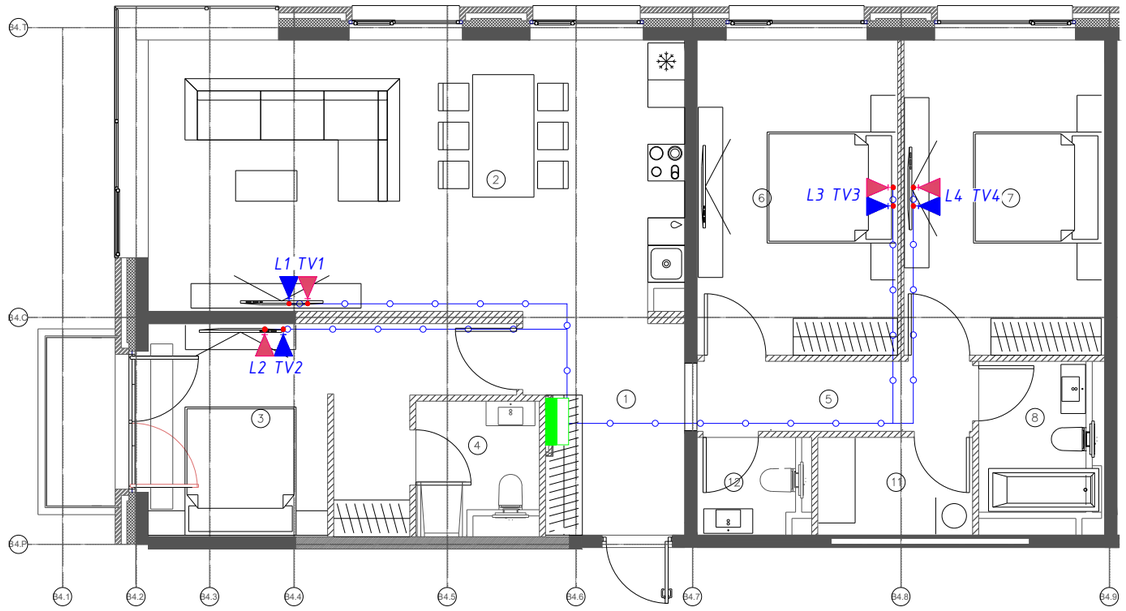

Условные обозначения

- Щит силовой
- Щит слаботочной сети
- Мастер-выключатель одноклавишный (на весь свет в квартире)
- Выключатель одноклавишный скрытой установки
- Выключатель двухклавишный скрытой установки
- Переключатель одноклавишный скрытой установки
- Переключатель двухклавишный скрытой установки
- Светильник (устанавливается собственником)
- Информационная розетка RJ45 cat.5e
- ТВ розетка
- Кабель ВВГнг(А)-LS 3х1,5 освещения
- Кабель слаботочной сети (см. кабельный журнал)

ЭТАЖ 9

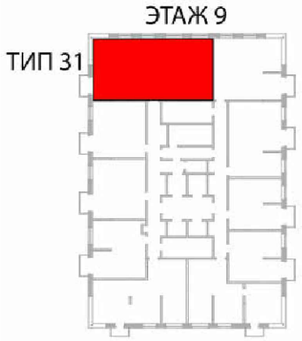

Кабельный журнал слаботочной сети

№ п/п	Откуда	Куда	Марка кабеля	Длина	Примечание
1	ЩСС	L1	UTP 4х2х0,5	15	
2	ЩСС	L2	UTP 4х2х0,5	15	
3	ЩСС	L3	UTP 4х2х0,5	17	
4	ЩСС	L4	UTP 4х2х0,5	17	
5	ЩСС	TV1	5D-FB	15	
6	ЩСС	TV2	5D-FB	15	
7	ЩСС	TV3	5D-FB	17	
8	ЩСС	TV4	5D-FB	17	

К ПРОИЗВОДСТВУ РАБОТ
25.02.2025
Главный инженер проекта
ООО ПЛАНЕТАСТРОЙ
С-77-247190
Отделкин Александр

Примечание:

1. Группы управления освещением 1-4 подключить на ЩС Гр.12
2. Группы управления освещением 5-12 подключить на ЩС Гр.13
3. Подключение светильников к выключателям (переключателям) выполнить в подрозетниках
4. Монтаж выключателей выполнить на +0,950 от УЧП, если не указано иное
5. Мастер-выключатель установить на +1,700 от УЧП.
6. Переключатели в спальнях возле кроватей выполнить на +0,700 от УЧП.

Изм.	Кол.уч.	Лист	№ док.	Подп.	Дата	02/10/23-ЭОМ			
						Рабочая документация интерьеров квартир жилого дома, корпуса 2.2 с подземной автостоянкой по адресу: г. Москва, вн. тер. г. муниципальный округ Пресненский, ул. Пресненский Вал, земельный участок 27/5			
Разработал						Система электроснабжения. Освещение	Стадия	Лист	Листов
							Р	11	
Н. Контр.						План освещения, слаботочной сети	М-Дизайн		

Взам. инв.N | Подпись и дата | Инв.N подл.

Формат А3

№ п/п	Наименование и техническая характеристика	Тип, марка обозначение документа и опросного листа	Код оборудования, изделия, материала	Завод-изготовитель	Единица измерения	Количество	единицы, кг	Примечание
1	2	3	4	5	6	7	8	9
	Щитовое оборудование							
	Щит силовой ЩС							
1	Корпус пластиковый ЩРВ-П-48 IP41 белый 48 модулей		TI5-50-V-048-31	IEK	шт	1		
2	Выключатель нагрузки (мини-рубильник) ВН-32 3Р 50А		MNV10-3-050	IEK	шт	1		
3	Автоматический выключатель ВА47-60М 3Р С 32А 6кА		MVA31-3-032-C	IEK	шт	2		
4	Выключатель дифференциальный (УЗО) ВД1-63 4Р 50А 30мА		MDV10-4-050-030	IEK	шт	2		
5	Автоматический выключатель дифф. тока С16 30мА 1Р		MVD12-1-016-C-030	IEK	шт	3		
6	Автоматический выключатель ВА47-60М 1Р С 25А 6кА		MVA31-1-025-C	IEK	шт	1		
7	Независимый расцепитель РН-47		MVA01D-RN	IEK	шт	1		
8	Автоматический выключатель ВА47-60М 1Р С 16А 6кА		MVA31-1-016-C	IEK	шт	6		
9	Автоматический выключатель ВА47-60М 1Р С 10А 6кА		MVA31-1-010-C	IEK	шт	2		
10	Контактор модульный КМ20-11М АС		MKK11-20-11	IEK	шт	1		
11	Кросс-модуль ШНК 4х7 3L+PEN		TF-DN10-4-07-100	IEK	шт	1		
	Кабельная продукция							
12	Кабель силовой ВВГнг(А)-LS	5х4	ГОСТ 31565-2012	Россия	м	17		
13	Кабель силовой ВВГнг(А)-LS	3х4	ГОСТ 31565-2012	Россия	м	17		
14	Кабель силовой ВВГнг(А)-LS	3х2,5	ГОСТ 31565-2012	Россия	м	370		
15	Кабель силовой ВВГнг(А)-LS	3х1,5	ГОСТ 31565-2012	Россия	м	180		
16	Витая пара U/UTP кат.5Е 4х2х0,52 solid LSZH		LC1-C5E04-121-T-P-R	ITK	м	64		
17	Кабель коаксиальный		5D-FB	Россия	м	64		
18	Провод ПУГВнг(А)-LS 1х2,5		ГОСТ 31565-2012	Россия	м	30		
	Прочие изделия и материалы							
19	Корпус встраиваемый мультимедиа 470х306 с розетками 220В		EZ9E312S2FIT	SE	шт	1		

К ПРОИЗВОДСТВУ РАБОТ
25.02.2025
Главный инженер проекта
ООО ПЛАНЕТАСТРОЙ
С-77-247190
Отделкин Александр
ЩГГ

Оборудование и материалы могут быть заменены на аналогичное, но с характеристиками не хуже проектных

Изм.	Кол.уч.	Лист	№ док.	Подп.	Дата
Разработал					
Н. Контр.					

02/10/23-ЭОМ.С

Рабочая документация интерьеров квартир жилого дома, корпуса 2.2 с подземной автостоянкой по адресу: г. Москва, вн. тер. г. муниципальный округ Пресненский, ул. Пресненский Вал, земельный участок 27/5

Система электроснабжения. Освещение	Стадия	Лист	Листов
	Р	12	
Спецификация оборудования, изделий и материалов	М-Дизайн		

Взам. инв.N | Подпись и дата | Инв.N подл.

Формат А3

№ п/п	Наименование и техническая характеристика	Тип, марка обозначение документа и опросного листа	Код оборудования, изделия, материала	Завод-изготовитель	Единица измерения	Количество	единицы, кг	Примечание
1	2	3	4	5	6	7	8	9
20	ДЕЛИТЕЛЬ ТВ х 6 под F разъём 5-1000 МГц		05-6024	REXANT	шт	1		
21	Коннектор UTP cat.5e		CS3-1C5EU	ITK	шт	4		
22	Подрозетник для бетонных стен, большой глубины, размер 73х66 мм		KPR 68	Электродеталь	шт	86		
23	Гофротруба ПВХ 25D		91925	ДКС	м	17		
24	Держатель с защелкой D25		51025	ДКС	шт	34		
25	Гофротруба ПВХ 20D		91920	ДКС	м	695		
26	Держатель с защелкой D20		51020	ДКС	шт	1390		
27	Труба ВГП D32		ГОСТ 3262 75	Россия	м	2		Проходки

К ПРОИЗВОДСТВУ РАБОТ
25.02.2025
Главный инженер проекта
ООО ПЛАНЕТАСТРОЙ
С-77-247190
Отделкин Александр

Взам. инв.N | Подпись и дата | Инв.N подл.

Изм.	Кол.	Лист	№ док.	Подпись	Дата

02/10/23-ЭОМ.С

Лист 13

Формат А3

Ведомость ссылочных и прилагаемых документов

Обозначение	Наименование	Примечание
	Ссылочные документы	
СП 30.13330.2020	Внутренний водопровод и канализация зданий	
СП 73.13330.2016	Внутренние санитарно-технические системы зданий	
СП 54.13330.2022	Здания жилые многоквартирные	
ГОСТ 21.601-2011	Правила выполнения рабочей документации внутренних систем...	
	Прилагаемые документы	
02/10/23-ВК.СО	Спецификация оборудования, изделий и материалов	
Приложение 1	Узел коллекторный водоснабжения "Пульсар" на 10/6 отводов	

Основные показатели систем водоснабжения и канализации

Наименование системы	Требуемое давление на вводе, МПа	Расчетный расход				Установочная мощность электродвига-телей, кВт	Примечание
		$м^3$/сут	$м^3$/ч	л/с	при пожаре, л/с		
В1 (ХВС)	0,2-0,45 МПа	0,660	0,778	1,33			
Т3 (ГВС)	0,2-0,45 МПа	0,420	0,460	0,63			

Технические решения принятые проектом в рабочих чертежах, соответствуют требованиям экологических, санитарно-гигиенических, противопожарных и других норм, действующих на территории Российской Федерации и обеспечивают безопасную для жизни и здоровья людей эксплуатацию объекта при соблюдении предусмотренных рабочими чертежами мероприятий.

Главный инженер проекта _____

К ПРОИЗВОДСТВУ РАБОТ
25.02.2025
Главный инженер проекта
ООО ПЛАНЕТАСТРОЙ
С-77-247190
Отделкин Александр

Согласовано

Взам. инв. №

Подп. и дата

Инв. № подл

Изм.	Кол. уч.	Лист	№ док.	Подпись	Дата
Архитектор					
Разработал		Сороков			

Шифр: 02/10/23-ВК
Заказчик: ООО «ПИК-УК»

Рабочая документация интерьеров квартир жилого дома, корпуса 2.2 с подземной автостоянкой по адресу: г. Москва, вн.тер.г. муниципальный округ Пресненский, улица Пресненский Вал, земельный участок 27/5

Водоснабжение и канализация. Этаж 9/ Квартира №2.2.0910	Стадия	Лист	Листов
	Р	14	
Общие данные (начало)	М-Дизайн		

Копировал

Формат

Общие указания

Проект водоснабжения и канализации (стадия "Р") разработан для типовой планировки квартиры (9-14 этаж, Тип 31) жилого дома, корпуса 2.2 с подземной автостоянкой по адресу : г. Москва, вн. тер. г. мун. округ Пресненский, ул. Пресненский Вал, земельный участок 27/5.

Проектная документация выполнена на основании технического задания и архитектурно- строительных чертежей. Рабочие чертежи разработаны в соответствии с действующими нормами, правилами и стандартами.

Система водоснабжения:

Водоснабжение бытовых приборов и сантехнических устройств осуществляется от этажного распределительного коллектора, расположенного в осях В4.Р/В4.7-В4.8.

На вводе трубопроводов горячего и холодного водоснабжения в квартиру проектом 1115-50-02-2.2-ВК1 предусмотрена квартирная станция водоснабжения "Пульсар" с запорной и регулирующей арматурой, системой защиты от протечек, распределительными коллекторами (от 6 до 10 выходов) для ХВС и ГВС.

От кваритной станции до каждого потребителя прокладывается отдельный трубопровод горячего и/или холодного водоснабжения. Подключение трубопроводов к запорной арматуре коллекторов осуществляется с помощью комбинированного переходника с накидной гайкой (16х1/2" ВР) и ниппеля латунного (1/2" НР-НР).

Для организации резервного источника горячего водоснабжения предусматривается возможность установки проточного водонагревателя мощностью 15кВт.
Переключение с сетевой горяячей воды на электронагреватель производится вручную.

В качестве трубопроводов применяются трубы из сшитого полиэтилена типа RAUTITAN Flex (PE-Xa Flex), производства компании "Rehau"запорная и регулирующая арматура - латунные фитинги.
Трубопроводы прокладываются скрыто в конструкциях пола и стен.
Трубопроводы холодного и горячего водоснабжения прокладываются в теплоизоляции типа Энергофлекс СУПЕР толщиной 9 мм, изготовляемой из вспененного каучука.

Система канализаации:

Отвод воды от бытовых приборов и сантехнических устройств организован по четырём стоякам К1-1, К1-4, К1-6 и К1-7 расположенным в осях В4.С/В4.7, В4.Р/В4.6, В4.Р/В4.7-В4.8, и В4.Р/В4.9 соответственно.

Отвод сточных вод от санитарно-технических приборов осуществляется системой К1 самотёком в существующую систему канализации здания.

Системы канализации запроектированы из пластмассовых ПВХ труб.

Трубопроводы прокладываются с уклоном в сторону выпусков открыто по полу и стенам.


Для подсоединения сантехнических приборов к системе канализации использовать специальные резиновые манжеты соответствующего диаметра для обеспечения герметичности системы, избежания подтеков и запаха.

В местах расположения ревизий и подсоединений к стоякам предусмотреть люки или съемные щиты для удобного обслуживания и прочистки.

Указания по монтажу:

Монтаж и испытание внутренних систем водоснабжения и канализации производить согласно СП 73.13330.2016 "Внутренние санитарно-технические системы" и действующим инструкциям, указаниям и правилам по технике безопасности.
Испытания на прочность и плотность системы водоснабжения проводятся гидростатическим методом при величине давления равной 1,5 избыточного рабочего давления согласно СП 73.13330.2016.

Испытания систем внутренней канализации должны выполняться методом пролива воды путем одновременного открытия 75% санитарных приборов, подключенных к проверяемому участку в течение времени, необходимого для его осмотра.
Выдержавшей испытание считается система, если при ее осмотре не обнаружено течи через стенки трубопроводов и места соединений.

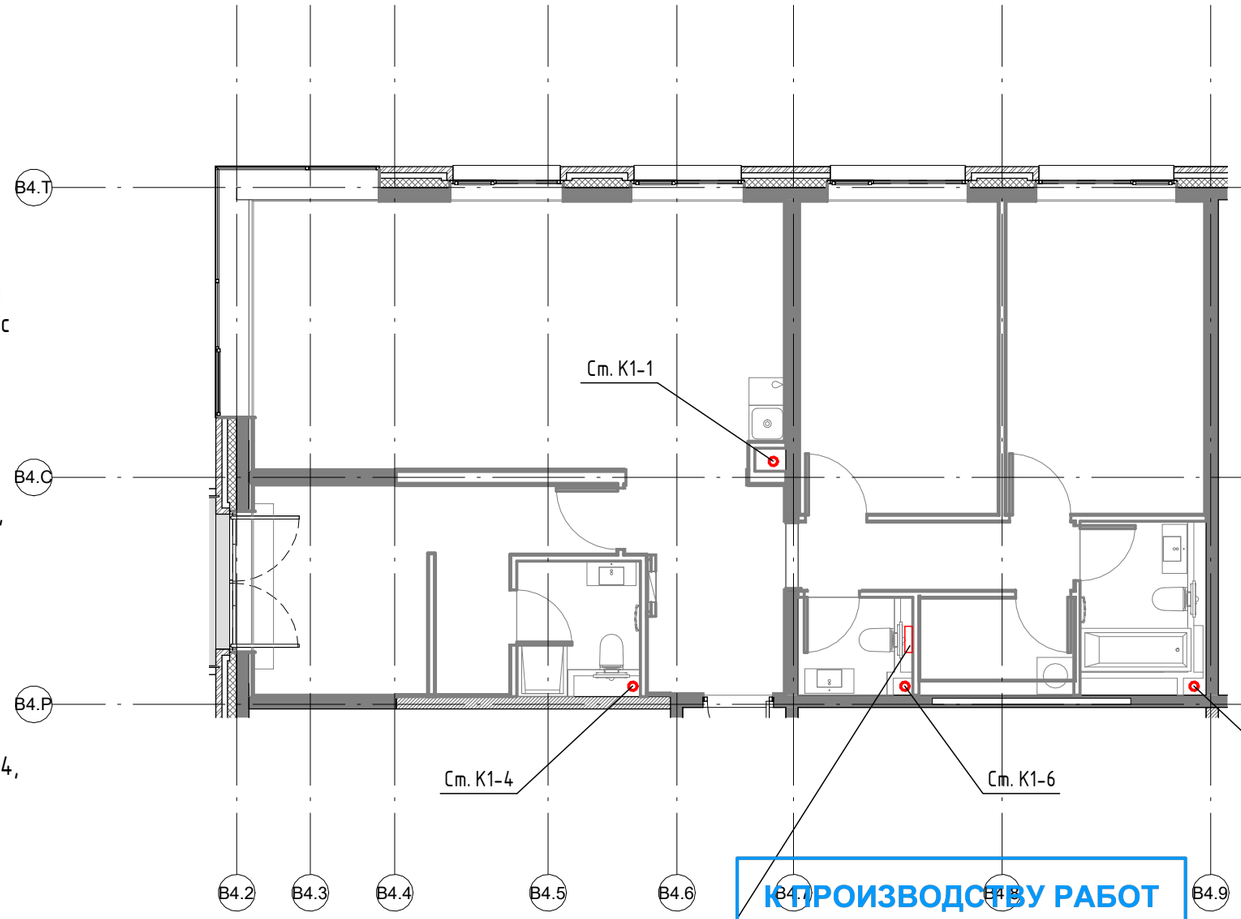

К ПРОИЗВОДСТВУ РАБОТ
25.02.2025
Главный инженер проекта
ООО ПЛАНЕТАСТРОЙ
С-77-247190
Отделкин Александр

Согласовано

Взам. инв №


Подп и дата

Инв. № подл

Изм.	Кол. уч.	Лист	№ док.	Подпись	Дата	Шифр: 02/10/23-ВК Заказчик: ООО «ПИК-УК»			
						Рабочая документация интерьеров квартир жилого дома, корпуса 2.2 с подземной автосоянкой по адресу: г. Москва, вн.тер.г. муниципальный округ Пресненский, улица Пресненский Вал, земельный участок 27/5			
Архитектор						Водоснабжение и канализация. Этаж 9/ Квартира №2.2.0910	Стадия	Лист	Листов
							Р	15	
Разработал		Сороков				Общие данные (окончание)	М-Дизайн		

Копировал

Формат

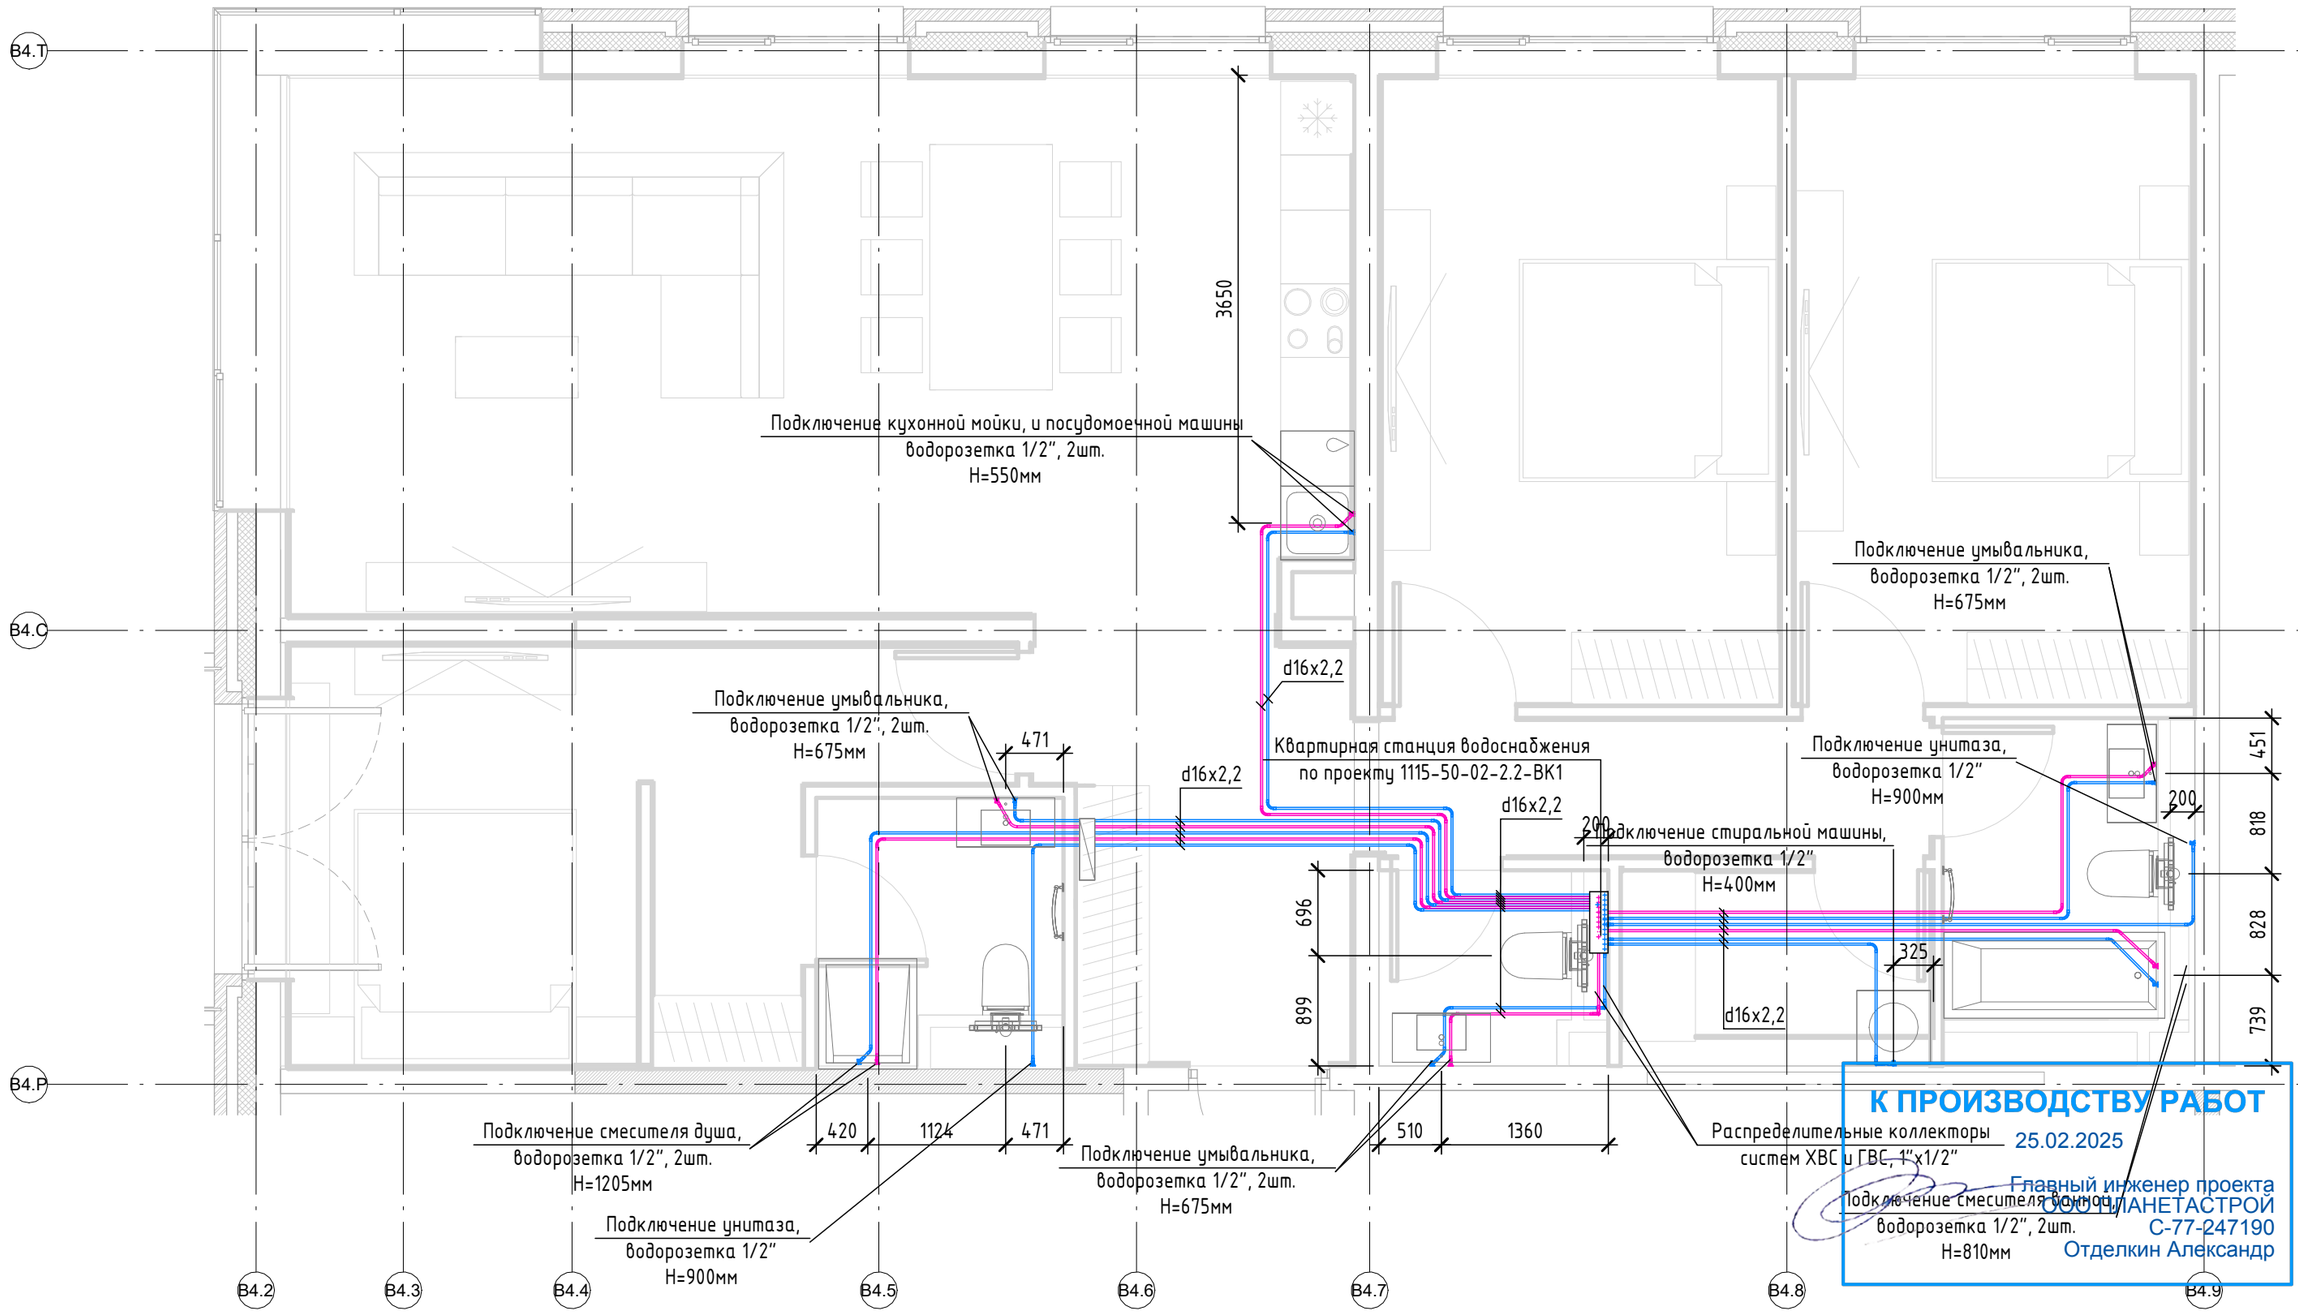

К ПРОИЗВОДСТВУ РАБОТ
25.02.2025
Главный инженер проекта
ООО "ПЛАНЕТАСТРОЙ"
С-77-247190
Отделкин Александр

Примечание:
1. Трубопроводы водоснабжения прокладываются в теплоизоляции из вспененного каучука толщиной 9 мм. Для систем холодного водоснабжения предусмотреть изоляцию синего цвета, для горячего водоснабжения - красного.
2. Для отводов трубопровода радиусом менее 4-х диаметров трубы следует использовать латунные фитинги.


Изм.	Кол. уч.	Лист	№ док.	Подпись	Дата
Архитектор					
Разработал		Сороков			

Шифр: 02/10/23-ВК
Заказчик: ООО «ПИК-УК»

Рабочая документация интерьеров квартир жилого дома, корпуса 2.2 с подземной автостоянкой по адресу: г. Москва, вн.тер.г. муниципальный округ Пресненский, улица Пресненский Вал, земельный участок 27/5

Водоснабжение и канализация. Этаж 9/ Квартира №2.2.0910	Стадия	Лист	Листов
	Р	16	
План систем водоснабжения М1-50	М-Дизайн		

Согласовано
Взам. инв №
Подп и дата
Инв № подл
Копировал
Формат

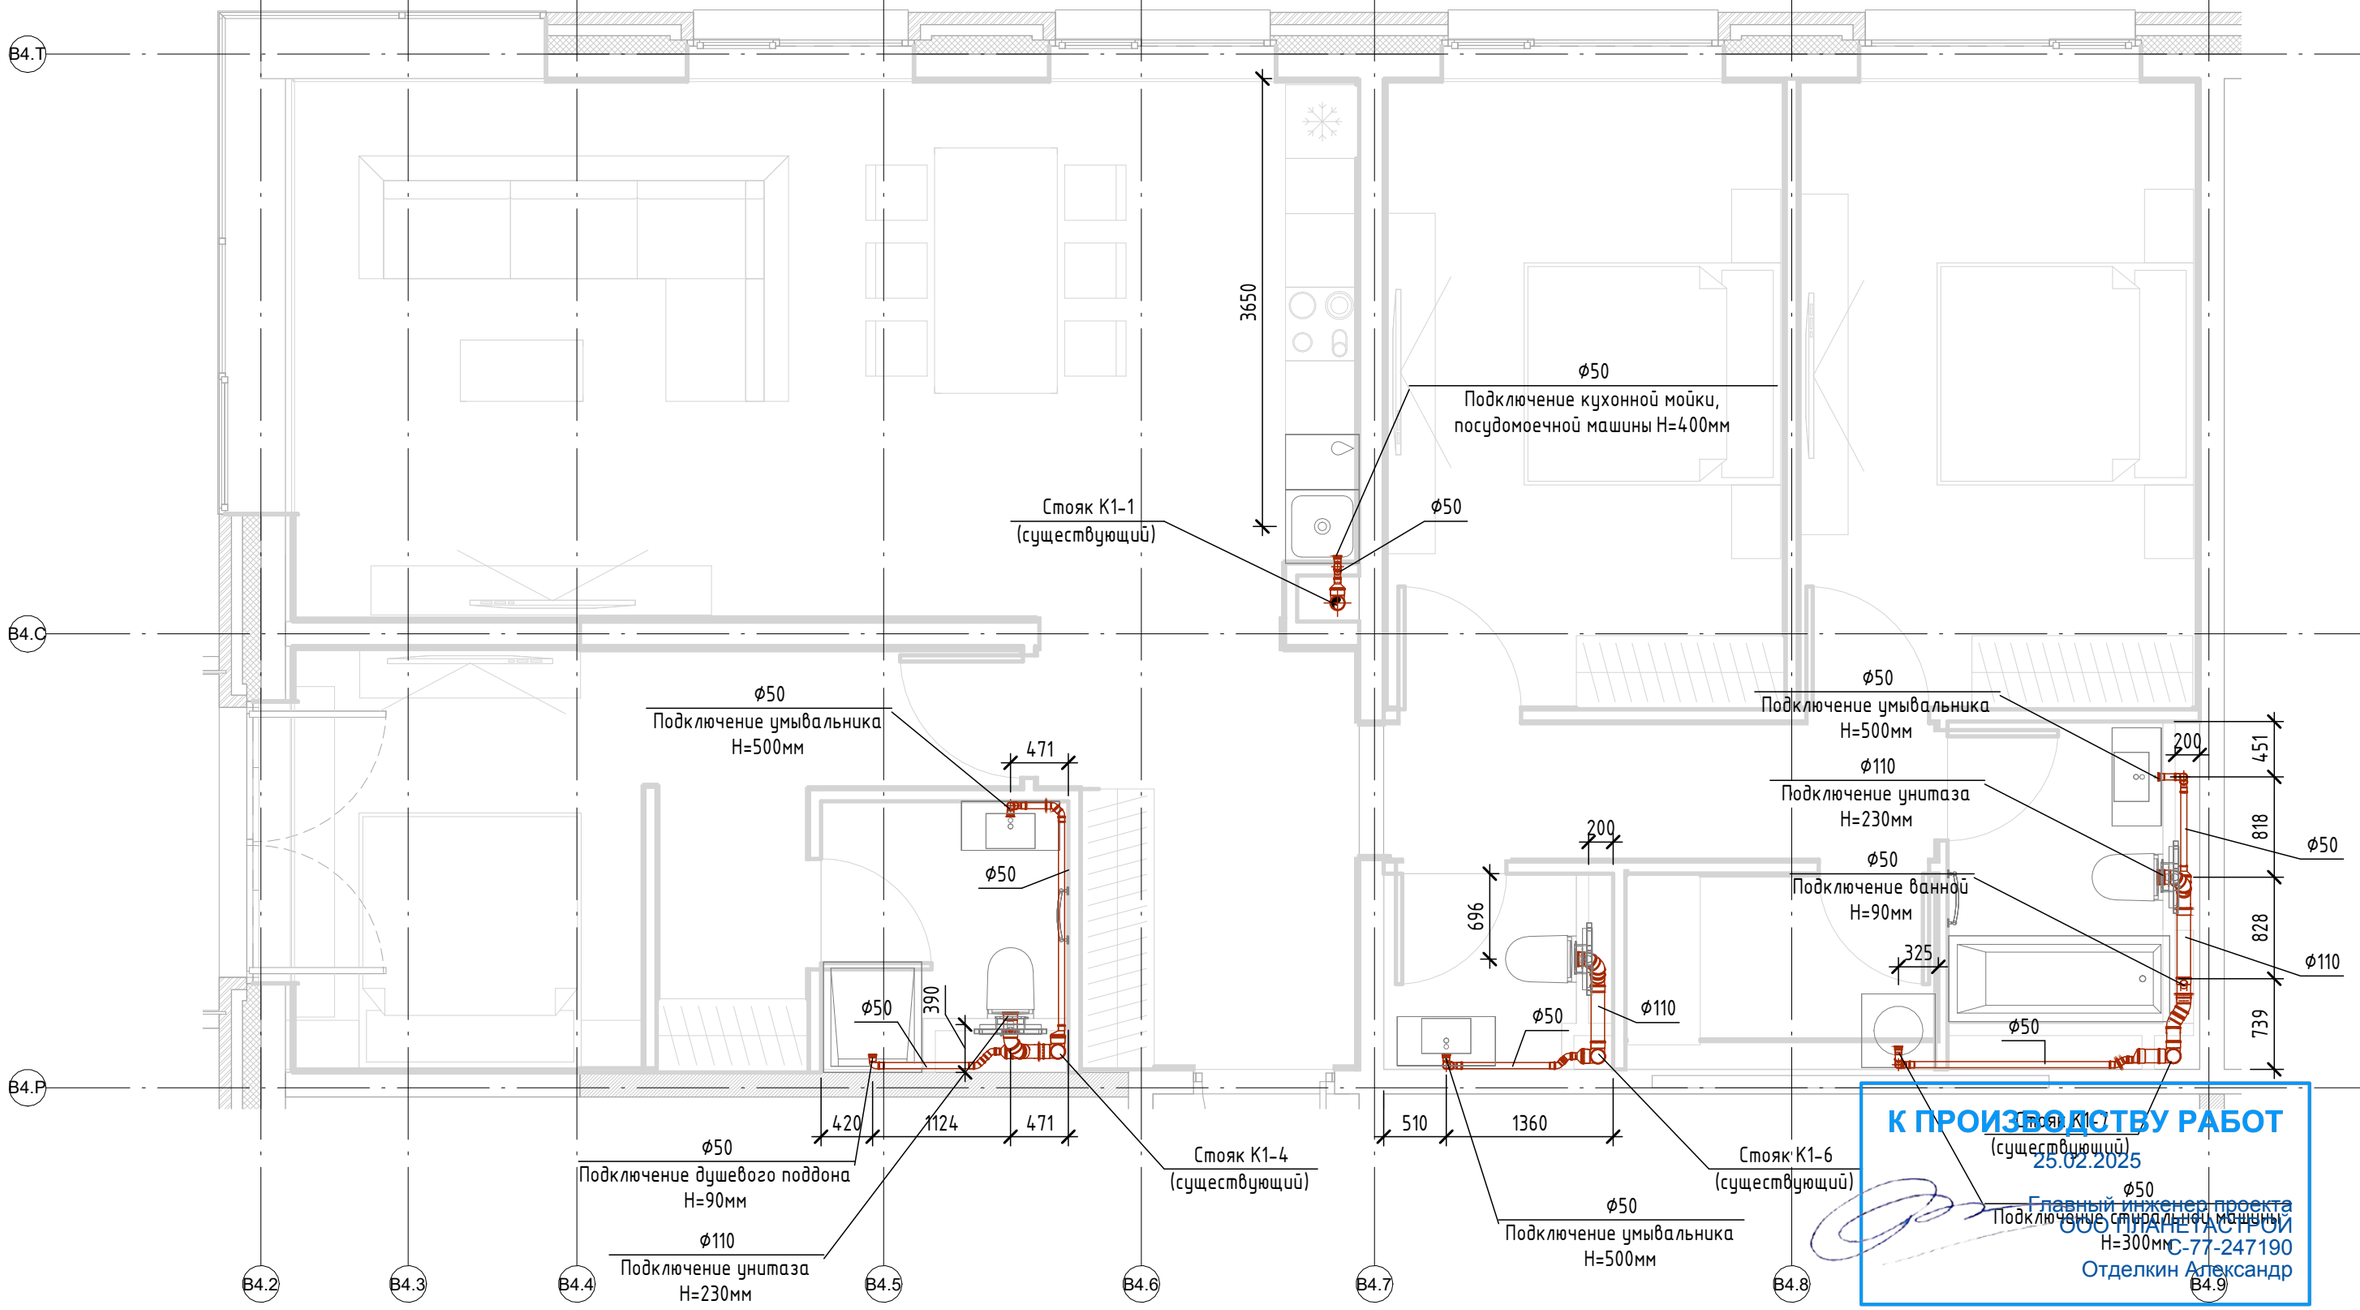

К ПРОИЗВОДСТВУ РАБОТ
25.02.2025
Главный инженер проекта
ООО "ПЛАНЕТАСТРОЙ"
С-77-247190
Отделкин Александр

Согласовано

Взам. инв №

Подп и дата

Инв. № подл

Изм.	Кол. уч.	Лист	№ док.	Подпись	Дата

Шифр: 02/10/23-ВК
Заказчик: ООО «ПИК-УК»

Рабочая документация интерьеров квартир жилого дома, корпуса 2.2 с подземной автосоянкой по адресу: г. Москва, вн.тер.г. муниципальный округ Пресненский, улица Пресненский Вал, земельный участок 27/5

Архитектор			
Разработал	Сороков		

Водоснабжение и канализация.
Этаж 9/ Квартира №2.2.0910


Стадия	Лист	Листов
Р	17	

План систем канализации М1-50

М-Дизайн

Копировал

Формат

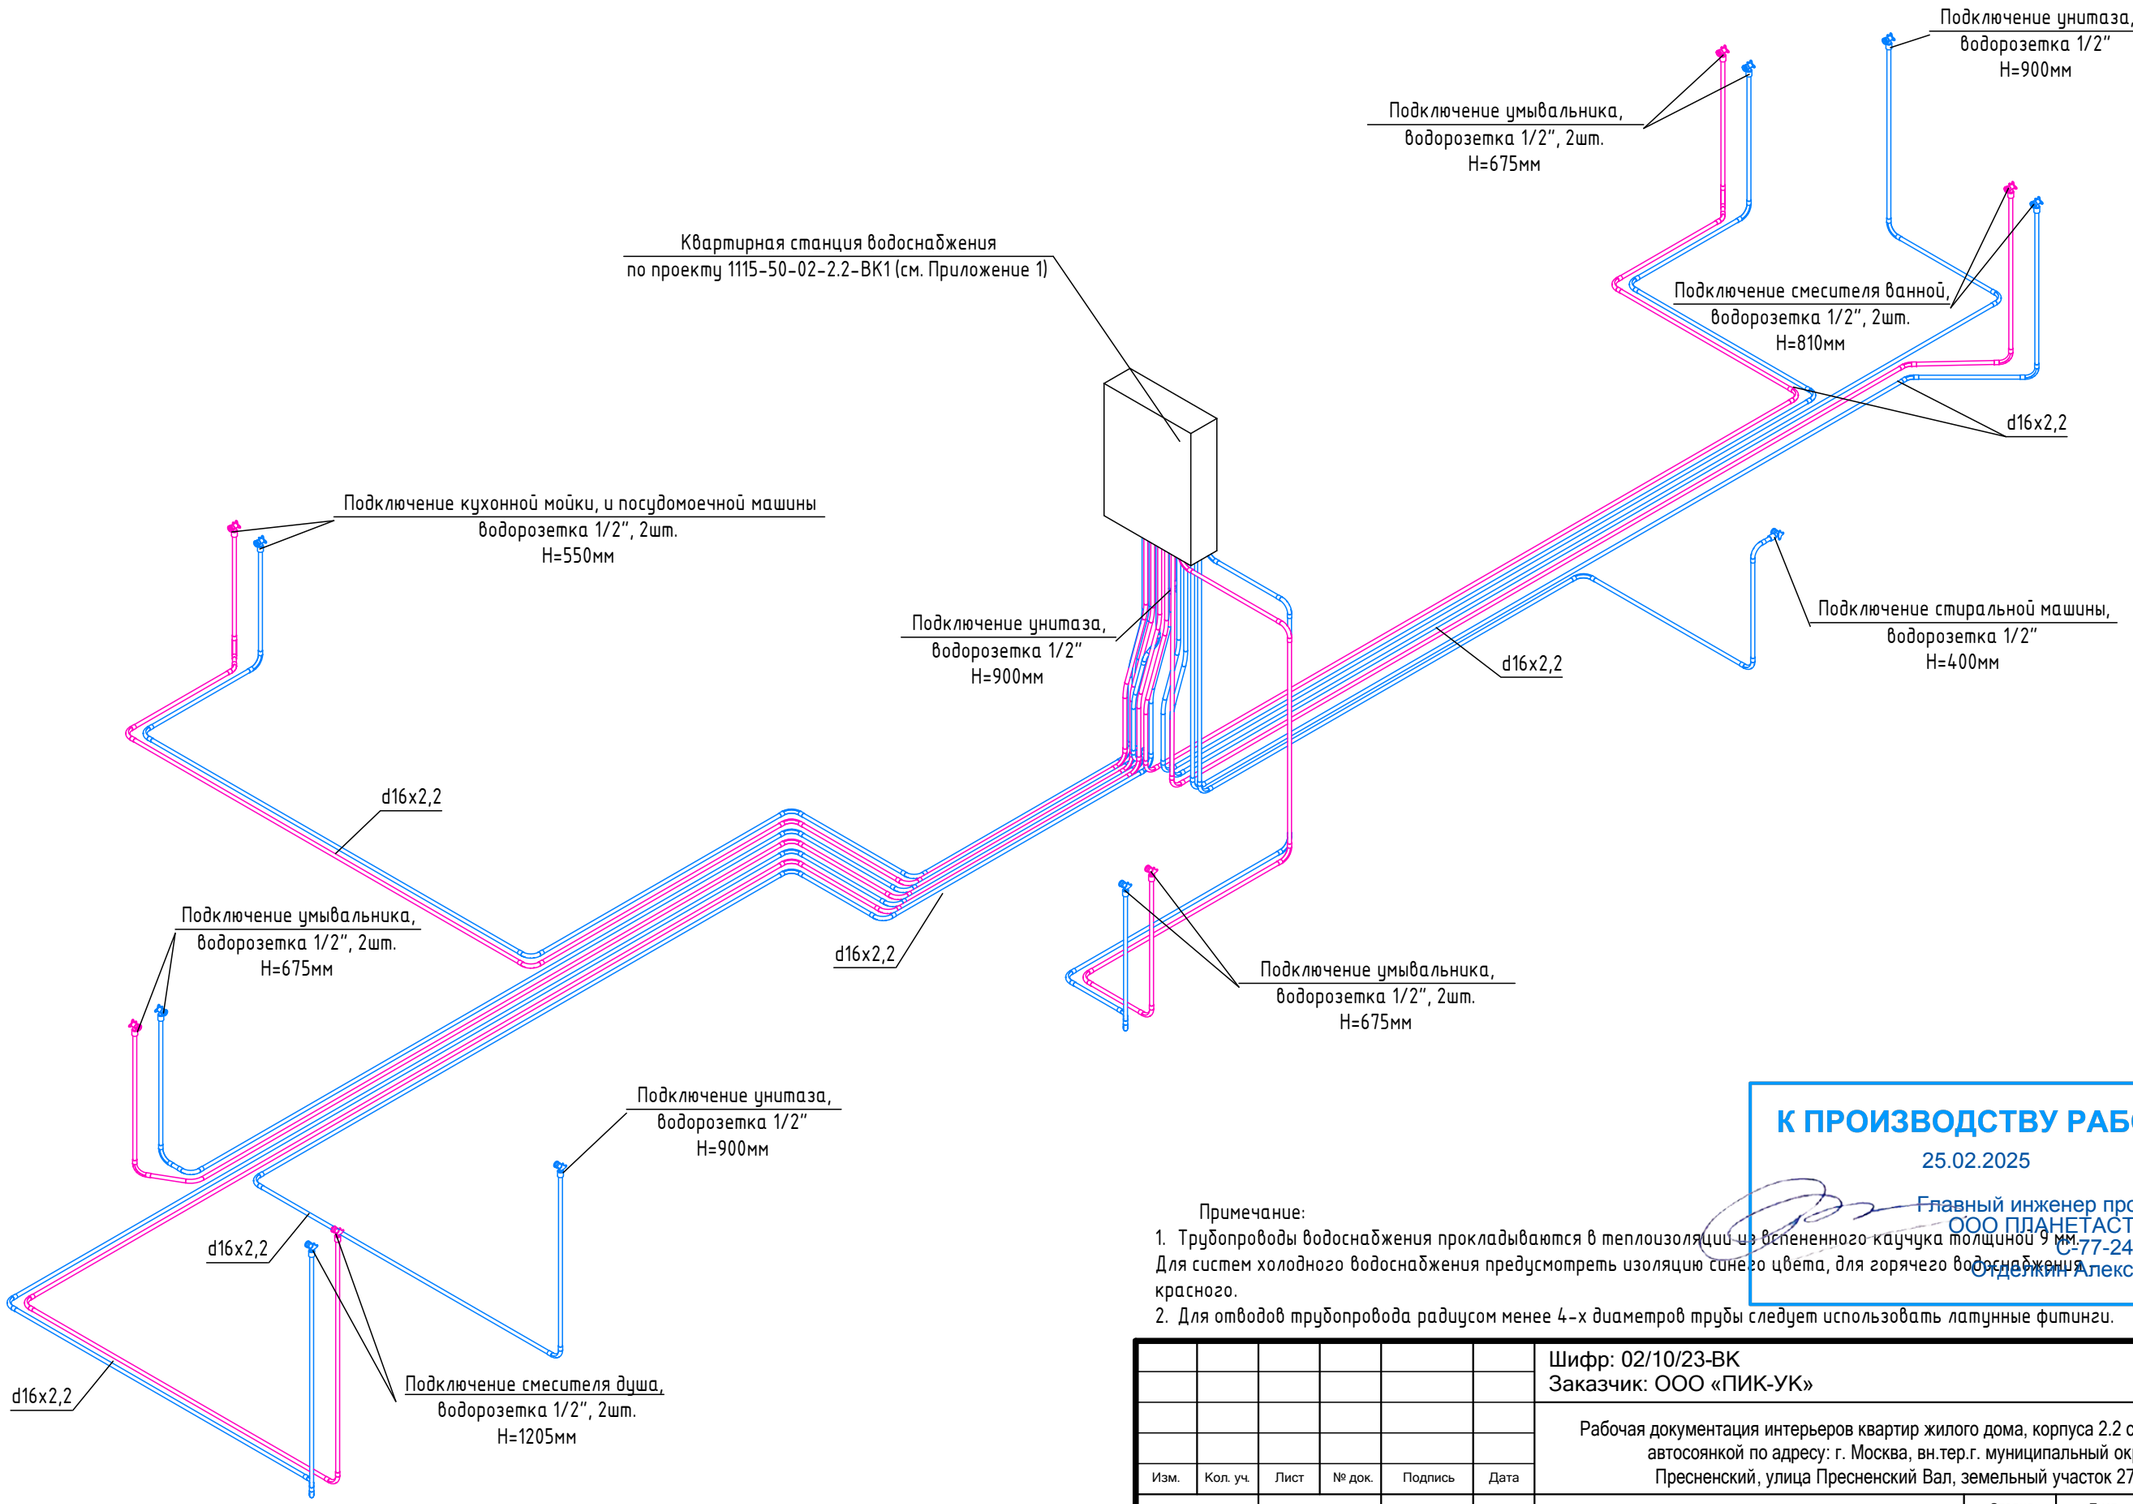

Примечание:

1. Трубопроводы водоснабжения прокладываются в теплоизоляции из вспененного каучука толщиной 9 мм. Для систем холодного водоснабжения предусмотреть изоляцию синего цвета, для горячего водоснабжения красного.
2. Для отводов трубопровода радиусом менее 4-х диаметров трубы следует использовать латунные фитинги.

К ПРОИЗВОДСТВУ РАБОТ
25.02.2025
Главный инженер проекта
ООО ПЛАНЕТАСТРОЙ
С-77-247190
Отделкин Александр

Изм.	Кол. уч.	Лист	№ док.	Подпись	Дата

Шифр: 02/10/23-ВК
Заказчик: ООО «ПИК-УК»

Рабочая документация интерьеров квартир жилого дома, корпуса 2.2 с подземной автосоянкой по адресу: г. Москва, вн.тер.г. муниципальный округ Пресненский, улица Пресненский Вал, земельный участок 27/5

Архитектор						Водоснабжение и канализация. Этаж 9/ Квартира №2.2.0910	Стадия	Лист	Листов
							Р	18	
Разработал		Сороков				Схемы систем водоснабжения	М-Дизайн		

Согласовано


Взам. инв №


Подп. и дата


Инв. № подл


Копировал

Формат

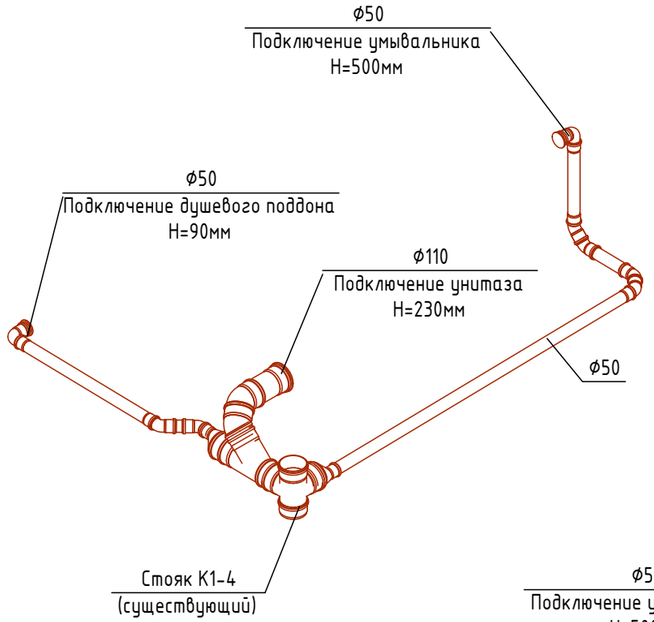

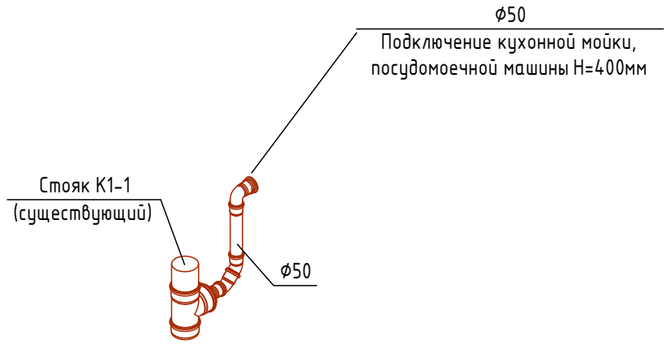

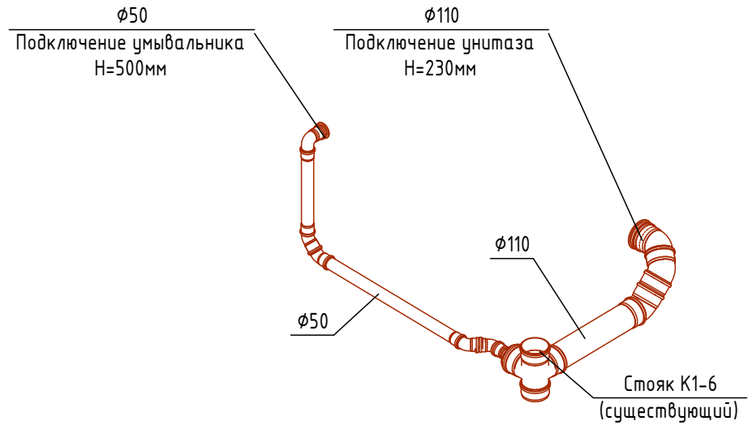

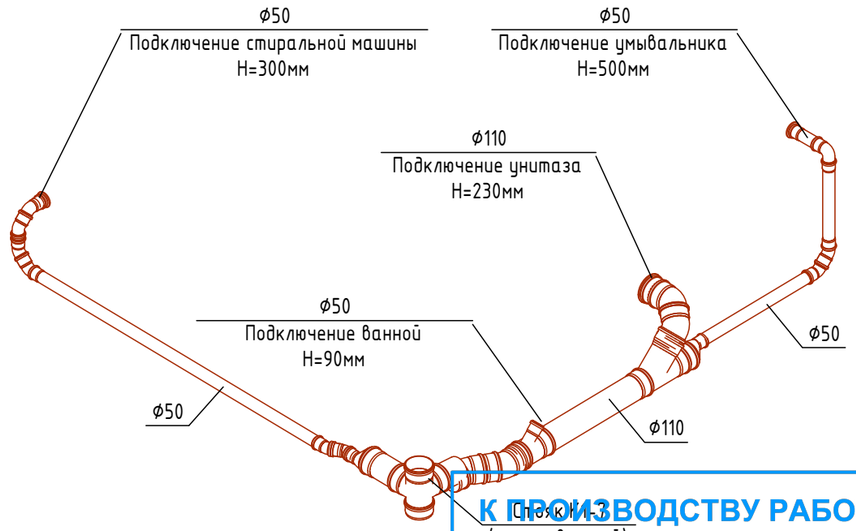

К ПРОИЗВОДСТВУ РАБОТ
25.02.2025
Главный инженер проекта
ООО ПЛАНЕТАСТРОЙ
С-77-247190
Отделкин Александр

Примечание:
1. Трубопроводы канализации прокладываются с уклоном не менее 0,2 см/м в сторону выпусков.

						Шифр: 02/10/23-ВК		
						Заказчик: ООО «ПИК-УК»		
						Рабочая документация интерьеров квартир жилого дома, корпуса 2.2 с подземной автосоянкой по адресу: г. Москва, вн.тер.г. муниципальный округ Пресненский, улица Пресненский Вал, земельный участок 27/5		
Изм.	Кол. уч.	Лист	№ док.	Подпись	Дата			
						Водоснабжение и канализация. Этаж 9/ Квартира №2.2.0910	Стадия: Р	Лист: 19 / Листов:
Архитектор								
Разработал		Сороков				Схемы систем канализации	М-Дизайн	

Согласовано

Взам. инв №

Подп. и дата

Инв. № подл

Копировал

Формат

Поз.	Наименование и техническая характеристика	Тип, марка, обозначение документа, опросного листа	Код изделия	Поставщик	Ед. изме-ре-ния	Кол-во	Масса 1 ед., кг.	Примечание
1	Ниппель с наружной резьбой	1/2"			шт	16		
2	Водорозетка надвижная с переходом на внутреннюю резьбу 16 х 1/2"				шт.	16	0.1	
3	Надвижная гильза для пресс-фитингов 16				шт.	32	0.008	
4	Направляющая 45[1] для фиксации поворота трубы 16				шт.	8	0.04	
5	Направляющая 90[1] для фиксации поворота трубы 16				шт.	66	0.055	
6	Переход напресовочный с накидной гайкой 16хG 1/2"				шт.	16	0.065	
7	Труба из сшитого полиэтилена ą16х2,2	RAUTITAN Flex		Rehau	м	111		
8	Трубки теплоизоляционные толщиной 9 мм для Ф16	Энергофлекс СУПЕР		Энергофлекс	м	111		

Согласовано

Взам. инв №

Подп и дата

Инв. № подл

К ПРОИЗВОДСТВУ РАБОТ
25.02.2025
Главный инженер проекта
ООО ПЛАНЕТАСТРОЙ
С-77-247190
Отделкин Александр

Изм.	Кол. уч.	Лист	№ док.	Подпись	Дата
Архитектор					
Разработал		Сороков			

Шифр: 02/10/23-ВК
Заказчик: ООО «ПИК-УК»

Рабочая документация интерьеров квартир жилого дома, корпуса 2.2 с подземной автосоянкой по адресу: г. Москва, вн.тер.г. муниципальный округ Пресненский, улица Пресненский Вал, земельный участок 27/5

Водоснабжение и канализация.
Этаж 9/ Квартира №2.2.0910

Стадия	Лист	Листов
Р	20	

Спецификация изделий и материалов

М-Дизайн

Копировал

Формат

Поз.	Наименование и техническая характеристика	Тип, марка, обозначение документа, опросного листа	Код изделия	Поставщик	Ед. измерения	Кол-во	Масса 1 ед., кг.	Примечание
1	Тройник канализационный 45[1] 110х110				шт.	2	0.38	
2	Тройник канализационный 45[1] 110х50				шт.	1	0.205	
3	Переход канализационный 110х50				шт.	6	0.115	
4	Отвод канализационный 90[1] 50				шт.	5	0.051	
5	Отвод канализационный 45[1] 110				шт.	7	0.18	
6	Отвод канализационный 45[1] 50				шт.	18	0.045	
7	Отвод канализационный 30[1] 110				шт.	2	0.17	
8	Отвод канализационный 30[1] 50				шт.	2	0.045	
9	Крестовина двухплоскостная канализационная 87.5[1] 110х110х110				шт.	3	0.31	
10	Заглушка канализационная 110				шт.	3	0.0612	
11	Заглушка канализационная 50				шт.	6	0.014	
12	Труба канализационная полипропиленовая ą50х1,8	ГОСТ 32414-2013			м	7.5		
13	Труба канализационная полипропиленовая ą110х2,7	ГОСТ 32414-2013			м	2		


Согласовано

Взам. инв. №

Подп. и дата

Инв. № подл.

К ПРОИЗВОДСТВУ РАБОТ
25.02.2025
Главный инженер проекта
ООО ПЛАНЕТАСТРОЙ
С-77-247190
Отделкин Александр

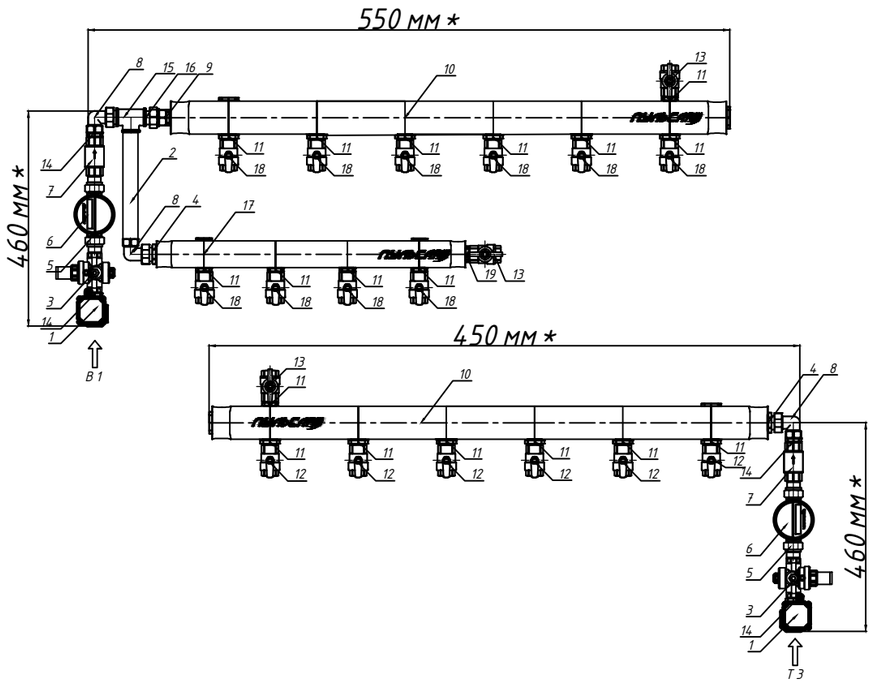

Узел коллекторный для водоснабжения «Пульсар» на 10/6 отводов:
0-Л/П-0-0-РД 20-25 НРЖ-10/6-15-0-0-К-0-0-0

№	Наименование	Артикул	Количество
1	Кран шаровый с электроприводом; Ду 20 В/В Gidrolock WI-FI WINNER (поставляется заказчиком)	Н 10024994	2
2	Сгон неразъемный; Ду 20; L=250	Н 10026031	1
3	Редуктор давления поршневой под манометр; радиальный; Ду 20; В/В Ру 16	Н 00076421	2
4	Футорка; Ду 25/Ду 20; Ру 40	Н 00004356	2
5	Комплект установочных присоединителей Ду 20	Н 00001458	2
6	Счетчик воды электронный унив. «Пульсар» Ду 20 RS-485 L130 кл.В модель 1	Н 00019600	2
7	Клапан обратный с латунным сердечником; Ду 20; Ру 10	Н 00014185	2
8	Американка угловая; Ду 20 В/Н Ру 40	Н 00025533	3
9	Ниппель переходной; Ду 25/Ду 20; Ру 40	Н 00010986	1
10	Коллектор из нержавеющей стали Ду 25; 6 отводов Ду 15, межосевое 50 мм	Н 10017066	2
11	Ниппель; Ду 15; Ру 16	Н 00004358	18
12	Кран шаровый "мини"; ручка-флажок красная; Ду 15 В/В; Ру 10	Н 10009811	6
13	Кран шаровый «Пульсар»; ручка-бабочка; Ду 15 В/В; Ру 16	Н 00006127	3
14	Ниппель; Ду 20; Ру 40	Н 00004359	4
15	Тройник с внутренней резьбой; Ду 20; Ру 40	Н 00014015	1
16	Американка; прямая; Ду 20; В/Н Ру 40	Н 00004337	1
17	Коллектор из нержавеющей стали Ду 25; 4 отвода Ду 15, межосевое 50 мм	Н 10011490	1
18	Кран шаровый "мини"; ручка-флажок синяяя; Ду 15 В/В; Ру 10	Н 10009812	10
19	Ниппель переходной; Ду 25/Ду 15; Ру 40	Н 00005513	1

*Указаны максимальные габаритные размеры.
Приборы учёта, указанные на схеме, не входят в фактический состав узла. Узел поставляется с монтажными вставками.
При сборке узлов могут использоваться дополнительные комплектующие, не отображенные в спецификации.
Возможное исполнение отводов: сварка/термосверление.
Уплотнение резьбовых соединений – анаэробный герметик.
Максимальная рабочая температура 95 °С.
Максимальное рабочее давление 10 бар.
Узлы имеют паспорт и сертификат.

Н 10024994 Кран шаровый с электроприводом; Ду 20 В/В Gidrolock WI-FI WINNER (поставляется заказчиком)

Согласовано _____ Дата 25.02.2025

Печать

К ПРОИЗВОДСТВУ РАБОТ
Главный инженер проекта
ООО ПЛАНЕТАСТРОЙ
С-77-247190
Отделкин Александр

ООО НПП "ТЕПЛОВОДОХРАН"
www.pulsarm.ru

Изм.	Лист	№ докум.	Подп.	Дата
Разраб.		Каширин		
Пров.		Князев		
Т.контр.				
Н.контр.				
Утв.				

Чертеж общего вида

Приложение 1

Лит.	Масса	Масштаб
Лист	Листов 1	

Перв. примен.
Справ. N°
Подп. и дата
Инв. N дубл.
Взам. инв. N°
Подп. и дата
Инв. N° подл.

Идентификатор документа 752047

Документ подписан электронной подписью в системе Vitro-CAD

Объект строительства ГП-2

Передан в Vitro-CAD 25.02.2025 11:56

Владелец	Сертификат	Дата подписания
Отделкин Александр Алексеевич Специалист ПОПИР	3A96E8670182E95E43F18E7C4F4947F6299AB075	25.02.2025 11:31